THE VALE OF
GLAMORGAN COUNCIL

TOWN AND COUNTRY PLANNING ACT 1990

APPROVED

SUBJECT TO COMPLIANCE WITH CONDITIONS (IF ANY)

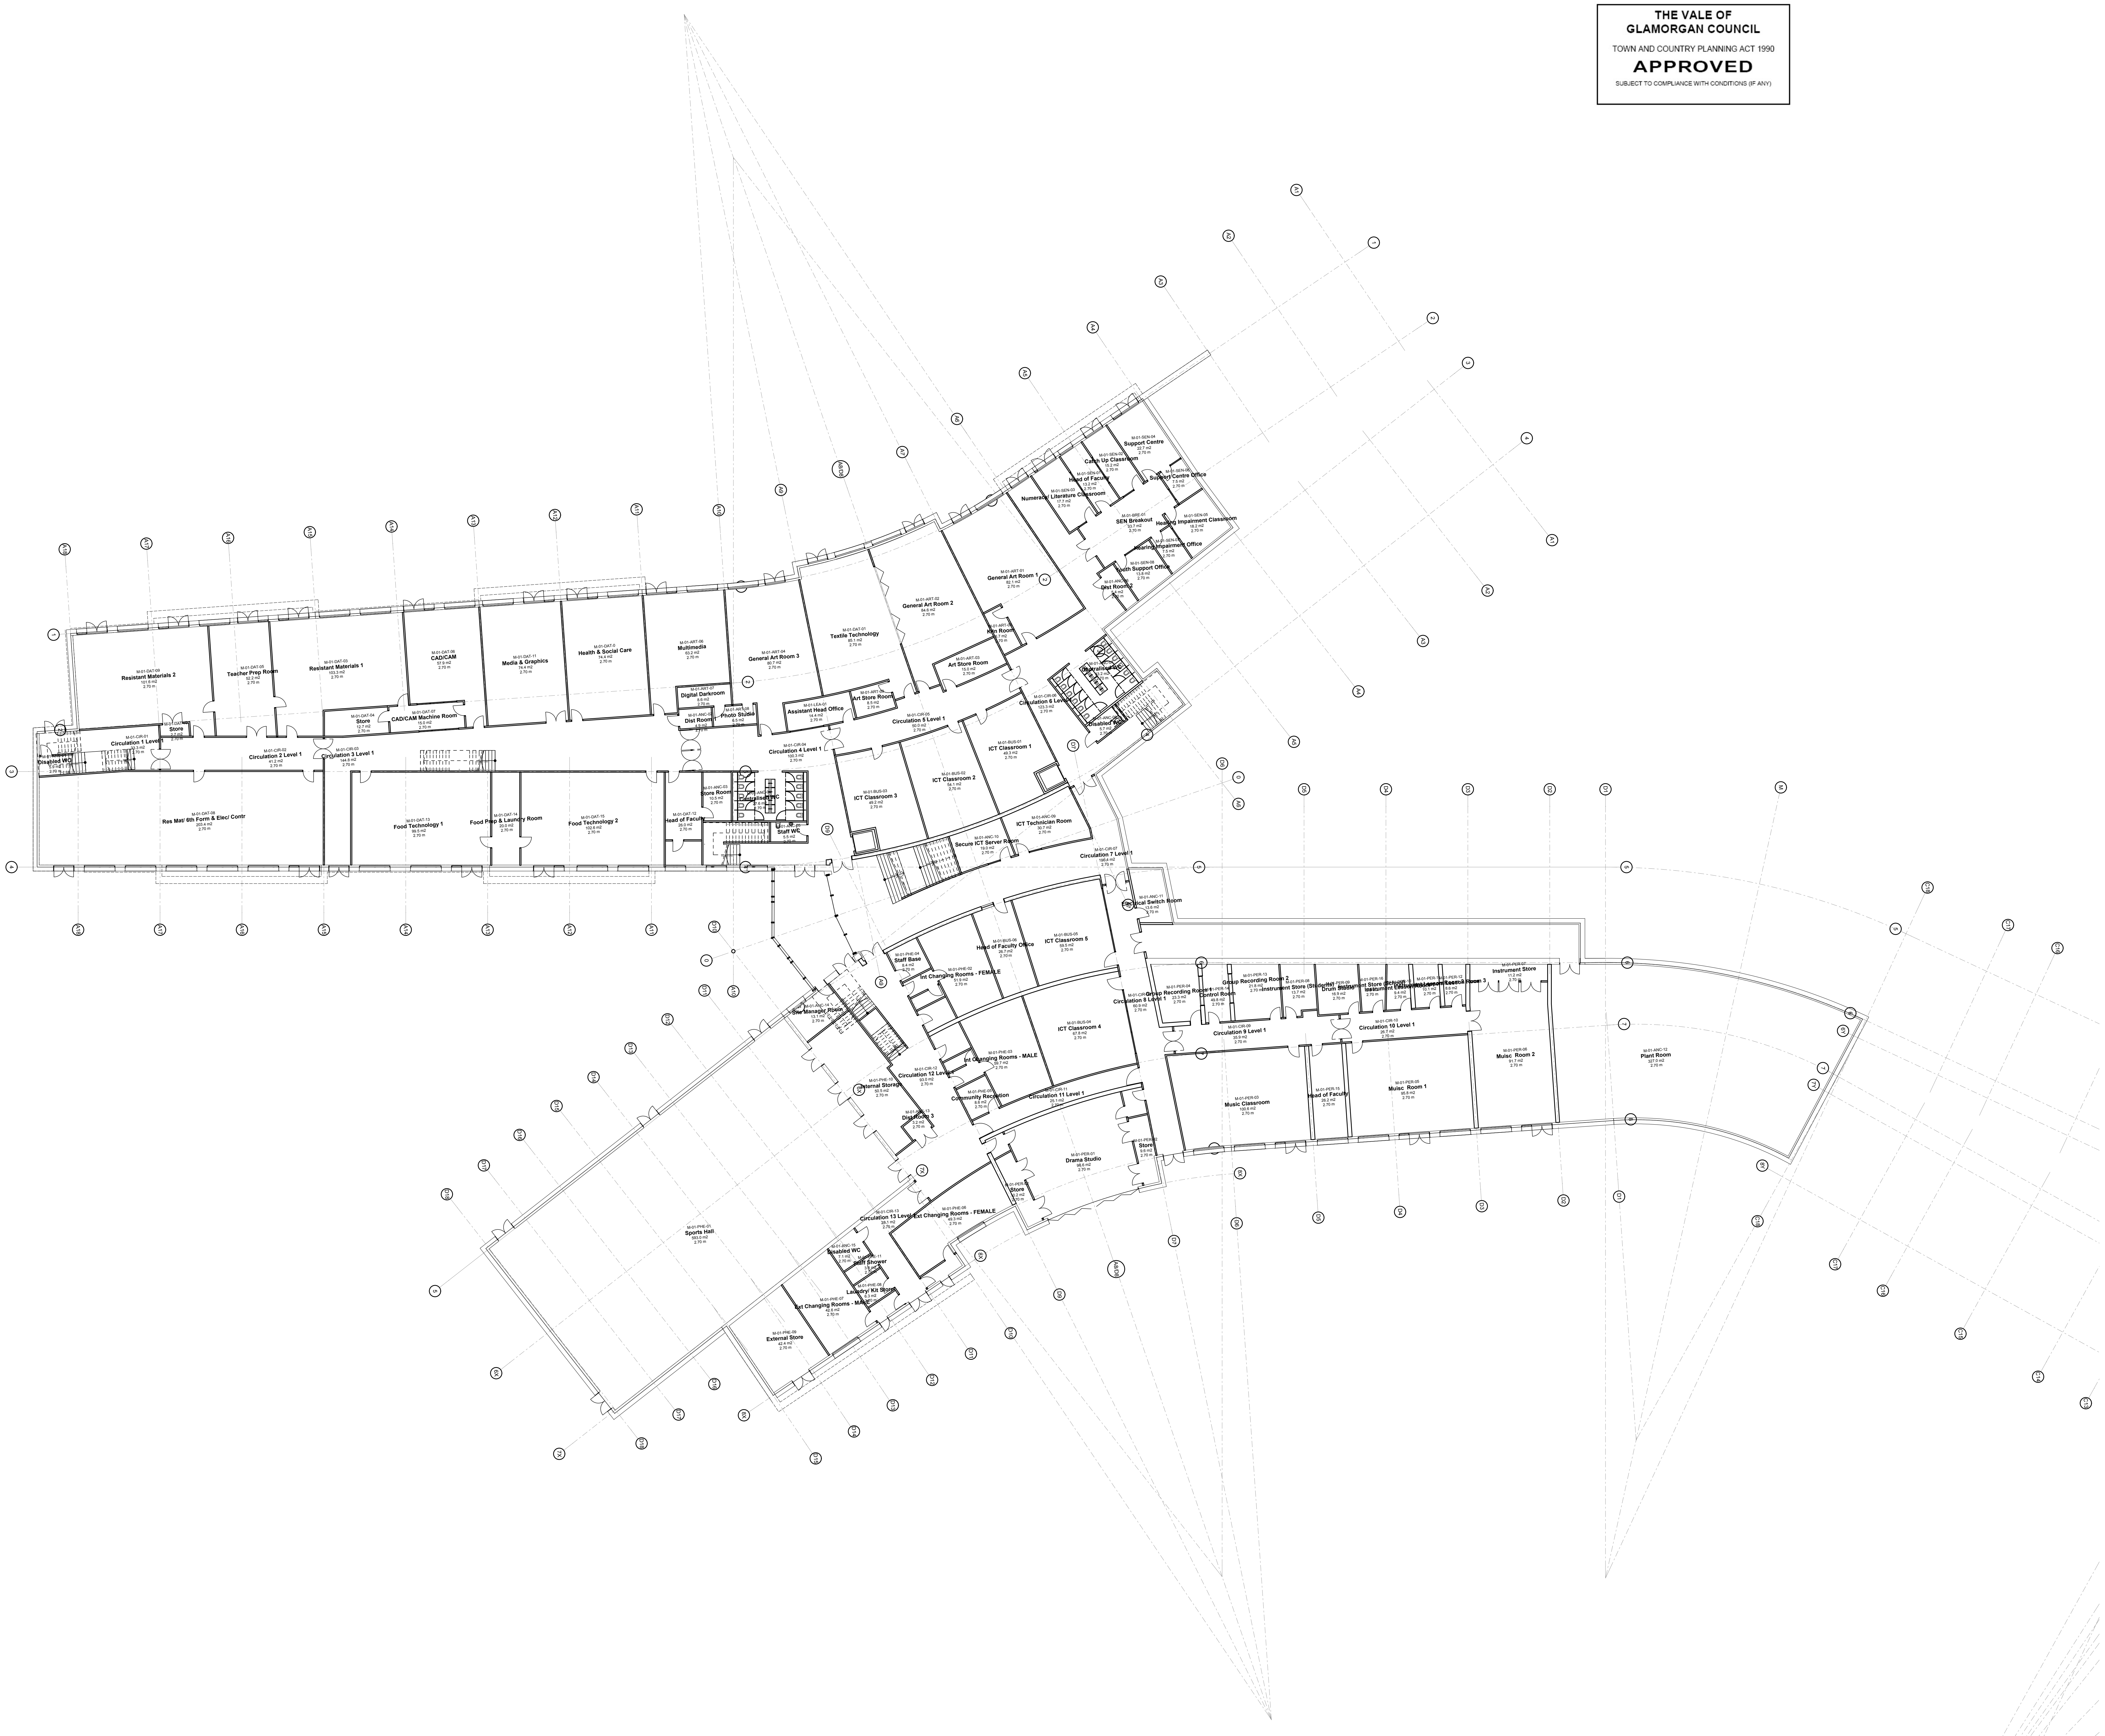
M-01-DAT-09 Resistant Materials 2 101.6 m2 2.70 m
M-01-DAT-05 Teacher Prep Room 52.2 m2 2.70 m
M-01-DAT-03 Resistant Materials 1 103.3 m2 2.70 m
M-01-DAT-06 CAD/CAM 57.9 m2 2.70 m
M-01-DAT-11 Media & Graphics 74.4 m2 2.70 m
M-01-DAT-0 Health & Social Care 74.4 m2 2.70 m
M-01-ART-06 Multimedia 63.2 m2 2.70 m
M-01-ART-04 General Art Room 3 80.7 m2 2.70 m
M-01-DAT-01 Textile Technology 85.1 m2 2.70 m
M-01-ART-02 General Art Room 2 84.6 m2 2.70 m
M-01-ART-01 General Art Room 1 82.1 m2 2.70 m
M-01-ART-05 Kiln Room 6.7 m2 2.70 m
M-01-ART-03 Art Store Room 15.0 m2 2.70 m
M-01-ART-09 Art Store Room 8.5 m2 2.70 m
M-01-LEA-01 Assistant Head Office 14.4 m2 2.70 m
M-01-ART-07 Digital Darkroom 8.6 m2 2.70 m
M-01-ART-08 Photo Studio 6.5 m2 2.70 m
M-01-ANC-02 Dist Room 1 4.9 m2 2.70 m
M-01-DAT-04 Store 12.7 m2 2.70 m
M-01-DAT-07 CAD/CAM Machine Room 15.0 m2 2.70 m
Store 2.7 m2 2.70 m
M-01-CIR-01 Circulation 1 Level 1 33.3 m2 2.70 m
Disabled WC 5.9 m2 2.70 m
M-01-CIR-02 Circulation 2 Level 1 41.2 m2 2.70 m
M-01-CIR-03 Circulation 3 Level 1 144.8 m2 2.70 m
M-01-CIR-04 Circulation 4 Level 1 100.3 m2 2.70 m
M-01-CIR-05 Circulation 5 Level 1 50.0 m2 2.70 m
M-01-CIR-06 Circulation 6 Level 1 123.3 m2 2.70 m
M-01-DAT-08 Res Mat/ 6th Form & Elec/ Contr 203.4 m2 2.70 m
M-01-DAT-13 Food Technology 1 99.5 m2 2.70 m
M-01-DAT-14 Food Prep & Laundry Room 20.0 m2 2.70 m
M-01-DAT-15 Food Technology 2 102.6 m2 2.70 m
M-01-DAT-12 Head of Faculty 26.0 m2 2.70 m
M-01-ANC-03 Store Room 10.5 m2 2.70 m
Centralised WC 27.6 m2 2.70 m
M-01-ANC-05 Staff WC 5.5 m2 2.70 m
M-01-BUS-03 ICT Classroom 3 49.2 m2 2.70 m
M-01-BUS-02 ICT Classroom 2 54.1 m2 2.70 m
M-01-BUS-01 ICT Classroom 1 49.3 m2 2.70 m
M-01-ANC-09 ICT Technician Room 30.7 m2 2.70 m
M-01-ANC-10 Secure ICT Server Room 19.0 m2 2.70 m
Centralised WC 33.2 m2 2.70 m
M-01-ANC-08 Disabled WC 5.7 m2 2.70 m
M-01-SEN-04 Support Centre 22.7 m2 2.70 m
M-01-SEN-02 Catch Up Classroom 15.2 m2 2.70 m
M-01-SEN-01 Head of Faculty 13.2 m2 2.70 m
M-01-SEN-06 Support Centre Office 7.5 m2 2.70 m
M-01-SEN-03 Numeracy/ Literature Classroom 17.7 m2 2.70 m
M-01-BRE-01 SEN Breakout 33.7 m2 2.70 m
M-01-SEN-05 Hearing Impairment Classroom 18.2 m2 2.70 m
M-01-SEN-07 Hearing Impairment Office 7.5 m2 2.70 m
M-01-SEN-08 Youth Support Office 13.8 m2 2.70 m
M-01-ANC-06 Dist Room 2 5.4 m2 2.70 m
M-01-CIR-07 Circulation 7 Level 1 196.4 m2 2.70 m
M-01-ANC-11 Electrical Switch Room 13.6 m2 2.70 m
M-01-BUS-05 ICT Classroom 5 59.5 m2 2.70 m
M-01-BUS-06 Head of Faculty Office 26.7 m2 2.70 m
M-01-PHE-04 Staff Base 8.4 m2 2.70 m
M-01-PHE-02 Int Changing Rooms - FEMALE 51.9 m2 2.70 m
M-01-BUS-04 ICT Classroom 4 67.8 m2 2.70 m
M-01-PHE-03 Int Changing Rooms - MALE 59.7 m2 2.70 m
M-01-PHE-05 Community Reception 8.6 m2 2.70 m
M-01-CIR-11 Circulation 11 Level 1 25.1 m2 2.70 m
M-01-CIR-08 Circulation 8 Level 1 60.9 m2 2.70 m
M-01-ANC-14 Site Manager Room 13.1 m2 2.70 m
M-01-CIR-12 Circulation 12 Level 1 93.0 m2 2.70 m
M-01-PHE-10 Internal Storage 50.5 m2 2.70 m
M-01-ANC-13 Dist Room 3 3.2 m2 2.70 m
M-01-PER-01 Drama Studio 96.6 m2 2.70 m
M-01-PER-02 Store 9.6 m2 2.70 m
Store 10.2 m2 2.70 m
M-01-CIR-13 Circulation 13 Level 1 28.1 m2 2.70 m
M-01-PHE-06 Ext Changing Rooms - FEMALE 49.3 m2 2.70 m
M-01-ANC-15 Disabled WC 7.1 m2 2.70 m
Staff Shower 3.8 m2 2.70 m
M-01-PHE-08 Laundry/ Kit Store 6.3 m2 2.70 m
M-01-PHE-07 Ext Changing Rooms - MALE 42.6 m2 2.70 m
M-01-PHE-09 External Store 42.4 m2 2.70 m
M-01-PHE-01 Sports Hall 593.0 m2 2.70 m
M-01-PER-04 Group Recording Room 1 23.3 m2 2.70 m
M-01-PER-14 Control Room 49.8 m2 2.70 m
M-01-PER-13 Group Recording Room 2 21.8 m2 2.70 m
M-01-PER-08 Instrument Store (Students) 13.7 m2 2.70 m
M-01-PER-09 Drum Studio 16.9 m2 2.70 m
M-01-PER-16 Instrument Store (School)
Instrument Lesson Room
M-01-PER-12 8.6 m2 2.70 m
M-01-PER-07 Instrument Store 11.2 m2 2.70 m
M-01-CIR-09 Circulation 9 Level 1 35.9 m2 2.70 m
M-01-CIR-10 Circulation 10 Level 1 26.7 m2 2.70 m
M-01-PER-03 Music Classroom 100.6 m2 2.70 m
M-01-PER-15 Head of Faculty 26.2 m2 2.70 m
M-01-PER-05 Muisc Room 1 95.8 m2 2.70 m
M-01-PER-06 Muisc Room 2 91.7 m2 2.70 m
M-01-ANC-12 Plant Room 327.0 m2 2.70 m

Notes

Check all dimensions on site. Do not scale from this drawing
Report any discrepancies and omissions to HLM Architects
This Drawing is Copyright ©

DESIGN/SKETCH DESIGN
Unless stated otherwise, the designs shown are subject to detailed site survey, investigations, and legal definition, the CDM Regulations, and the comments and / or approval of the various relevant Local Authority Officers, Statutory Undertakers, Fire Officers, Engineers and the like. They are copyright, project specific and confidential and no part is to be used or copied in any way without the express prior consent of HLM Architects.

PHOTOCOPIED/SCANNED INFORMATION
NB This drawing is based on photocopied / scanned information liable to distortion in scale.

AREA CALCULATIONS
NB The areas shown are approximate only and have been measured off preliminary drawings as the likely areas at the current state of design using the stated option from the Code of Measuring Practice, 4th edition. RICS / ISVA. These may be affected by future design development and construction tolerances, or the result of surveys for existing buildings. Take account of these factors before planning any financial or property development purpose or strategy and seek confirmation of latest areas before decision making.

3RD-PARTY INFORMATION
NB This drawing includes information provided by independent surveyors and / or consultants, to whom all queries shall be made. HLM Architects can accept no liability for its content or accuracy.

M 20 40 60 80 1:1250
1 1 2 3 1:50/1:20
0.5 0.5

Rev Description	Date	Drn	Chk
Issued for Planning	04/04/12	MR	PG

Project

PENARTH LEARNING COMMUNITY

Client

Title

MAINSTREAM SCHOOL LEVEL 1 FLOOR PLAN

Drawing No.		Revision
08013 /	1L(05)001	PA1

Scale @ A0	Drawn
1:200	MLL
Date	**Checked**
05/01/2012	HLM

HLM
2nd Floor, Greyfriars House,
Greyfriars Road,
Cardiff, CF10 3AL
T: +44 (0)29 2039 6070
F: +44 (0)29 2039 6080
E: cardiff@hlmarchitects.com
Architecture
Landscape & Urban Design
Interiors
Environment
www.hlmarchitects.com
LONDON SHEFFIELD GLASGOW BELFAST CARDIFF PLYMOUTH ABU DHABI SOUTH AFRICA