THE VALE OF
GLAMORGAN COUNCIL

TOWN AND COUNTRY PLANNING ACT 1990

APPROVED

SUBJECT TO COMPLIANCE WITH CONDITIONS (IF ANY)

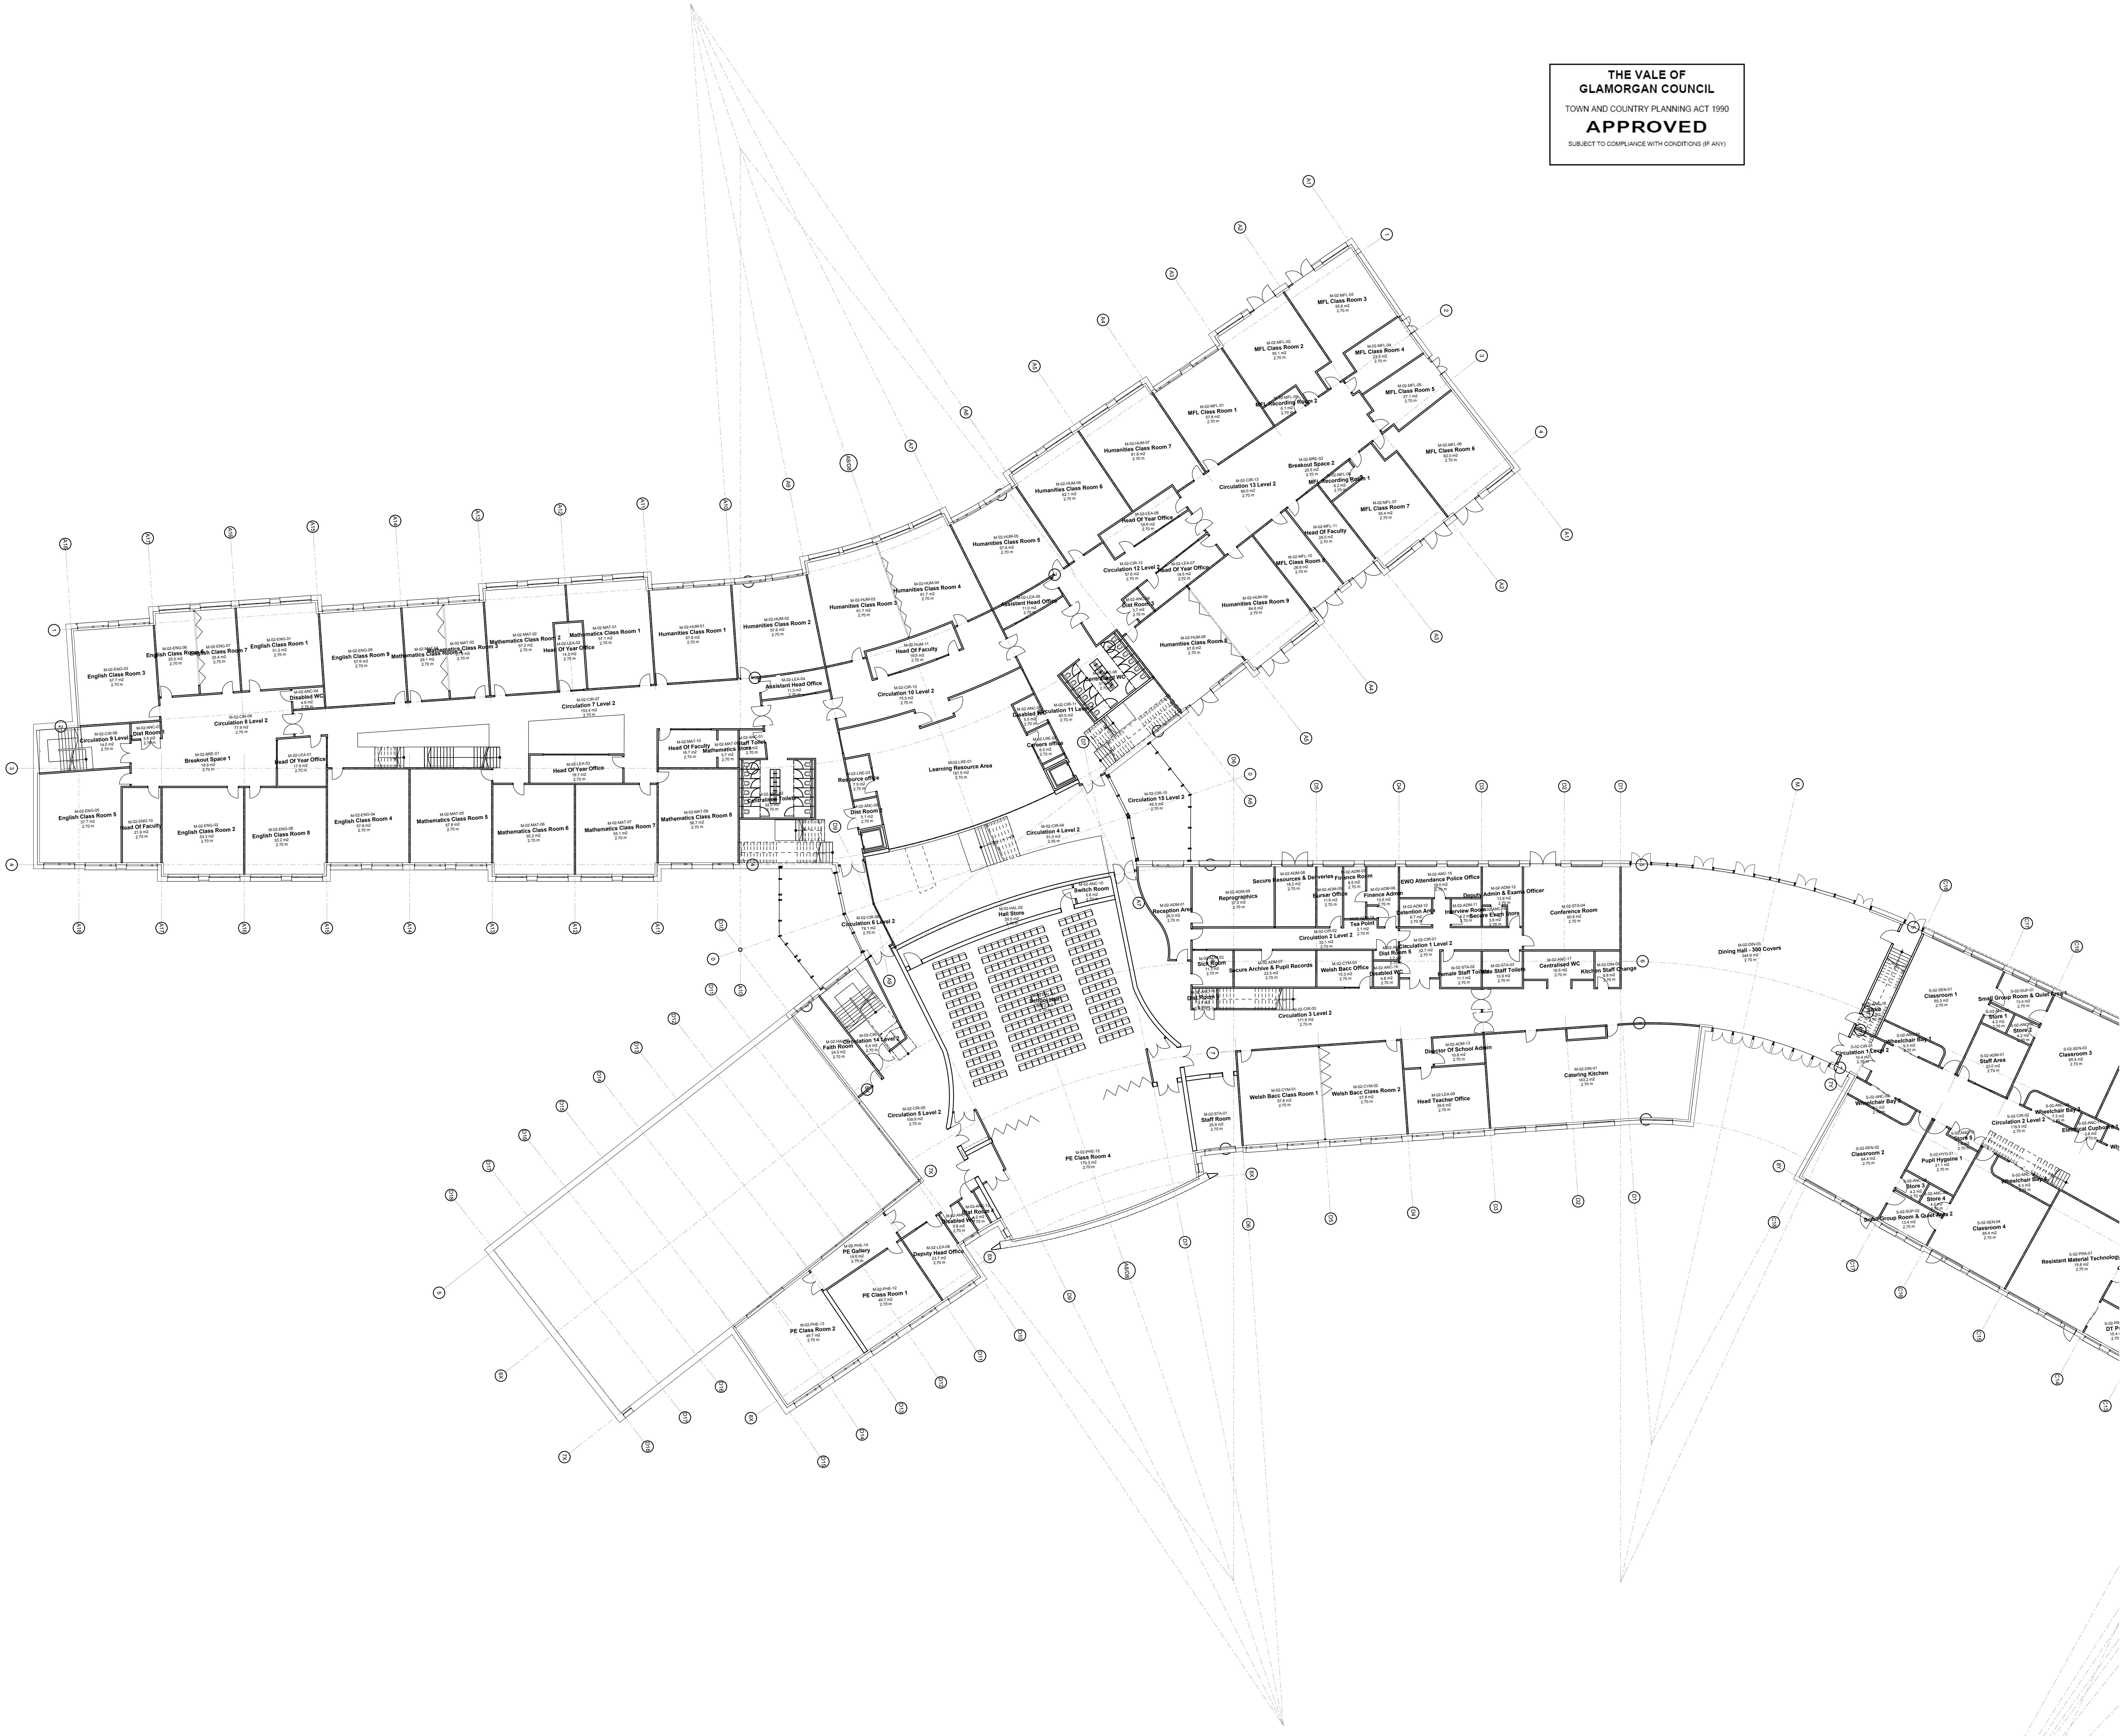
M-02-ENG-03 English Class Room 3 57.7 m2 2.70 m
M-02-ENG-06 English Class Room 6 25.0 m2 2.70 m
M-02-ENG-07 English Class Room 7 25.4 m2 2.70 m
M-02-ENG-01 English Class Room 1 51.2 m2 2.70 m
M-02-ENG-09 English Class Room 9 57.6 m2 2.70 m
M-02-MAT-04 Mathematics Class Room 4 29.1 m2 2.70 m
M-02-MAT-03 Mathematics Class Room 3 27.8 m2 2.70 m
M-02-MAT-02 Mathematics Class Room 2 57.2 m2 2.70 m
M-02-LEA-02 Head Of Year Office 14.2 m2 2.70 m
M-02-MAT-01 Mathematics Class Room 1 57.1 m2 2.70 m
M-02-HUM-01 Humanities Class Room 1 57.8 m2 2.70 m
M-02-HUM-02 Humanities Class Room 2 57.6 m2 2.70 m
M-02-HUM-03 Humanities Class Room 3 61.7 m2 2.70 m
M-02-HUM-04 Humanities Class Room 4 61.7 m2 2.70 m
M-02-HUM-05 Humanities Class Room 5 57.6 m2 2.70 m
M-02-HUM-06 Humanities Class Room 6 62.1 m2 2.70 m
M-02-HUM-07 Humanities Class Room 7 61.8 m2 2.70 m
M-02-MFL-01 MFL Class Room 1 57.8 m2 2.70 m
M-02-MFL-02 MFL Class Room 2 55.1 m2 2.70 m
M-02-MFL-03 MFL Class Room 3 55.6 m2 2.70 m
M-02-MFL-04 MFL Class Room 4 23.5 m2 2.70 m
M-02-MFL-05 MFL Class Room 5 27.1 m2 2.70 m
M-02-MFL-06 MFL Class Room 6 62.0 m2 2.70 m
M-02-MFL-07 MFL Class Room 7 55.4 m2 2.70 m
M-02-MFL-09 MFL Recording Room 2 6.1 m2 2.70 m
M-02-MFL-08 MFL Recording Room 1 6.2 m2 2.70 m
M-02-BRE-02 Breakout Space 2 20.5 m2 2.70 m
M-02-CIR-13 Circulation 13 Level 2 89.0 m2 2.70 m
M-02-MFL-11 Head Of Faculty 28.0 m2 2.70 m
M-02-MFL-10 MFL Class Room 8 28.8 m2 2.70 m
M-02-LEA-06 Head Of Year Office 18.6 m2 2.70 m
M-02-CIR-12 Circulation 12 Level 2 57.6 m2 2.70 m
M-02-LEA-07 Head Of Year Office 18.5 m2 2.70 m
M-02-ANC-09 Dist Room 3 3.7 m2 2.70 m
M-02-HUM-09 Humanities Class Room 9 64.6 m2 2.70 m
M-02-HUM-08 Humanities Class Room 8 57.8 m2 2.70 m
M-02-ANC-08 Centralised WC 31.2 m2 2.70 m
M-02-LEA-05 Assistant Head Office 11.0 m2 2.70 m
M-02-HUM-11 Head Of Faculty 19.5 m2 2.70 m
M-02-LEA-04 Assistant Head Office 11.3 m2 2.70 m
M-02-CIR-10 Circulation 10 Level 2 75.5 m2 2.70 m
M-02-CIR-11 Circulation 11 Level 2 60.5 m2 2.70 m
M-02-ANC-06 Disabled WC 5.5 m2 2.70 m
M-02-LRE-02 Careers office 6.0 m2 2.70 m
M-02-LRE-01 Learning Resource Area 157.5 m2 2.70 m
M-02-LRE-03 Resource office 7.5 m2 2.70 m
M-02-ANC-05 Dist Room 2 5.1 m2 2.70 m
M-02-CIR-04 Circulation 4 Level 2 51.0 m2 2.70 m
M-02-CIR-15 Circulation 15 Level 2 45.5 m2 2.70 m
M-02-CIR-06 Circulation 6 Level 2 78.1 m2 2.70 m
M-02-ENG-05 English Class Room 5 57.7 m2 2.70 m
M-02-ENG-10 Head Of Faculty 21.9 m2 2.70 m
M-02-ENG-02 English Class Room 2 53.3 m2 2.70 m
M-02-ENG-08 English Class Room 8 53.2 m2 2.70 m
M-02-ENG-04 English Class Room 4 57.8 m2 2.70 m
M-02-MAT-05 Mathematics Class Room 5 57.8 m2 2.70 m
M-02-MAT-06 Mathematics Class Room 6 55.2 m2 2.70 m
M-02-MAT-07 Mathematics Class Room 7 55.1 m2 2.70 m
M-02-MAT-08 Mathematics Class Room 8 56.7 m2 2.70 m
M-02-LEA-03 Head Of Year Office 19.7 m2 2.70 m
M-02-MAT-10 Head Of Faculty 16.7 m2 2.70 m
M-02-MAT-09 Mathematics Store 5.7 m2 2.70 m
M-02-ANC-01 Staff Toilet 2.70 m
M-02-ANC-02 Centralised Toilets 32.0 m2 2.70 m
M-02-CIR-07 Circulation 7 Level 2 153.4 m2 2.70 m
M-02-CIR-08 Circulation 8 Level 2 77.9 m2 2.70 m
M-02-CIR-09 Circulation 9 Level 2 14.0 m2 2.70 m
M-02-ANC-03 Dist Room 1 3.5 m2 2.70 m
M-02-BRE-01 Breakout Space 1 18.9 m2 2.70 m
M-02-LEA-01 Head Of Year Office 17.9 m2 2.70 m
M-02-ANC-04 Disabled WC 4.9 m2 2.70 m
M-02-ANC-10 Switch Room 5.6 m2 2.70 m
M-02-HAL-02 Hall Store 28.5 m2 2.70 m
School Hall 2.70 m
Faith Room 24.0 m2 2.70 m
M-02-CIR-14 Circulation 14 Level 2 6.4 m2 2.70 m
M-02-CIR-05 Circulation 5 Level 2 109.9 m2 2.70 m
M-02-PHE-15 PE Class Room 4 170.3 m2 2.70 m
M-02-ANC-12 Dist Room 4 4.2 m2 2.70 m
Disabled WC 5.8 m2 2.70 m
M-02-LEA-08 Deputy Head Office 23.7 m2 2.70 m
M-02-PHE-14 PE Gallery 19.6 m2 2.70 m
M-02-PHE-12 PE Class Room 1 49.7 m2 2.70 m
M-02-PHE-13 PE Class Room 2 49.7 m2 2.70 m
M-02-STA-01 Staff Room 25.9 m2 2.70 m
M-02-ADM-01 Reception Area 26.0 m2 2.70 m
M-02-ADM-09 Reprographics 37.0 m2 2.70 m
M-02-ADM-08 Secure Resources & Deliveries 18.2 m2 2.70 m
M-02-ADM-03 Finance Room 8.5 m2 2.70 m
M-02-ADM-05 Bursar Office 11.6 m2 2.70 m
M-02-ADM-06 Finance Admin 13.5 m2 2.70 m
M-02-ADM-04 Tea Point 2.1 m2 2.70 m
M-02-ANC-15 EWO Attendance Police Office 19.0 m2 2.70 m
M-02-ADM-12 Deputy Admin & Exams Officer 13.9 m2 2.70 m
M-02-ADM-10 Detention Area 6.7 m2 2.70 m
M-02-ADM-11 Interview Room 6.2 m2 2.70 m
M-02-ANC-16 Secure Exam Store 3.6 m2 2.70 m
M-02-STA-04 Conference Room 60.6 m2 2.70 m
M-02-CIR-02 Circulation 2 Level 2 33.1 m2 2.70 m
M-02-CIR-01 Circulation 1 Level 2 32.7 m2 2.70 m
Dist Room 5 1.7 m2 2.70 m
M-02-ADM-02 Sick Room 11.3 m2 2.70 m
M-02-ADM-07 Secure Archive & Pupil Records 22.5 m2 2.70 m
M-02-CYM-03 Welsh Bacc Office 15.3 m2 2.70 m
M-02-ANC-14 Disabled WC 4.8 m2 2.70 m
M-02-STA-02 Female Staff Toilets 11.1 m2 2.70 m
M-02-STA-03 Male Staff Toilets 10.9 m2 2.70 m
M-02-ANC-17 Centralised WC 16.6 m2 2.70 m
M-02-DIN-02 Kitchen Staff Change 6.8 m2 2.70 m
M-02-ANC-19 Dist Room 6 3.7 m2 2.70 m
M-02-CIR-03 Circulation 3 Level 2 171.6 m2 2.70 m
M-02-ADM-13 Director Of School Admin 10.8 m2 2.70 m
M-02-CYM-01 Welsh Bacc Class Room 1 57.8 m2 2.70 m
M-02-CYM-02 Welsh Bacc Class Room 2 57.8 m2 2.70 m
M-02-LEA-09 Head Teacher Office 39.6 m2 2.70 m
M-02-DIN-01 Catering Kitchen 143.2 m2 2.70 m
M-02-DIN-03 Dining Hall - 300 Covers 344.9 m2 2.70 m
M-02-ANC-18 Store 2.70 m
S-02-SEN-01 Classroom 1 65.3 m2 2.70 m
S-02-SUP-01 Small Group Room & Quiet Area 1 13.4 m2 2.70 m
S-02-ANC-06 Store 1 4.2 m2 2.70 m
S-02-ANC-07 Store 2 4.2 m2 2.70 m
S-02-ADM-01 Staff Area 23.0 m2 2.70 m
S-02-SEN-03 Classroom 3 65.4 m2 2.70 m
S-02-ANC-01 Wheelchair Bay 1 9.3 m2 2.70 m
S-02-CIR-01 Circulation 1 Level 2 10.4 m2 2.70 m
S-02-ANC-02 Wheelchair Bay 2 9.1 m2 2.70 m
S-02-CIR-02 Circulation 2 Level 2 119.5 m2 2.70 m
S-02-ANC-03 Wheelchair Bay 3 7.3 m2 2.70 m
S-02-ANC-11 Electrical Cupboard 1 3.8 m2 2.70 m
S-02-ANC-10 Store 5 1.4 m2 2.70 m
S-02-SEN-02 Classroom 2 64.4 m2 2.70 m
S-02-HYG-01 Pupil Hygeine 1 21.1 m2 2.70 m
S-02-ANC-08 Store 3 4.2 m2 2.70 m
S-02-ANC-09 Store 4 4.2 m2 2.70 m
S-02-ANC-04 Wheelchair Bay 4 9.3 m2 2.70 m
S-02-SUP-02 Small Group Room & Quiet Area 2 13.4 m2 2.70 m
S-02-SEN-04 Classroom 4 65.4 m2 2.70 m
S-02-PRA-01 Resistant Material Technology 75.6 m2 2.70 m

1:1250
1:50/1:20

Notes

Check all dimensions on site. Do not scale from this drawing
Report any discrepancies and omissions to HLM Architects
This Drawing is Copyright ©

DESIGN/SKETCH DESIGN
Unless stated otherwise, the designs shown are subject to detailed site survey, investigations, and legal definition, the CDM Regulations, and the comments and / or approval of the various relevant Local Authority Officers, Statutory Undertakers, Fire Officers, Engineers and the like. They are copyright, project specific and confidential and no part is to be used or copied in any way without the express prior consent of HLM Architects.

PHOTOCOPIED/SCANNED INFORMATION
NB This drawing is based on photocopied / scanned information liable to distortion in scale.

AREA CALCULATIONS
NB The areas shown are approximate only and have been measured off preliminary drawings as the likely areas at the current state of design using the stated option from the Code of Measuring Practice, 4th edition. RICS / ISVA. These may be affected by future design development and construction tolerances, or the result of surveys for existing buildings. Take account of these factors before planning any financial or property development purpose or strategy and seek confirmation of latest areas before decision making.

3RD-PARTY INFORMATION
NB This drawing includes information provided by independent surveyors and / or consultants, to whom all queries shall be made. HLM Architects can accept no liability for its content or accuracy.

Rev Description	Date	Drn	Chk
Issued for Planning	04/01/12	MR	PG

Project

PENARTH LEARNING COMMUNITY

Client

Title

MAINSTREAM SCHOOL LEVEL 2 FLOOR PLAN

Drawing No.	Revision
08013 / 1L(05)002	PA1

Scale @ A0	Drawn
1:200	MLL

Date	Checked
05/01/2012	HLM

HLM

2nd Floor, Greyfriars House,
Greyfriars Road,
Cardiff, CF10 3AL
T: +44 (0)29 2039 6070
F: +44 (0)29 2039 6080
E: cardiff@hlmarchitects.com
Architecture
Landscape & Urban Design
Interiors
Environment
www.hlmarchitects.com

LONDON SHEFFIELD GLASGOW BELFAST **CARDIFF** PLYMOUTH ABU DHABI SOUTH AFRICA

M 20 40 60 80 1:1250
1 1 2 3 0.5 0.5 1:50/1:20