THE VALE OF
GLAMORGAN COUNCIL
TOWN AND COUNTRY PLANNING ACT 1990
APPROVED
SUBJECT TO COMPLIANCE WITH CONDITIONS (IF ANY)

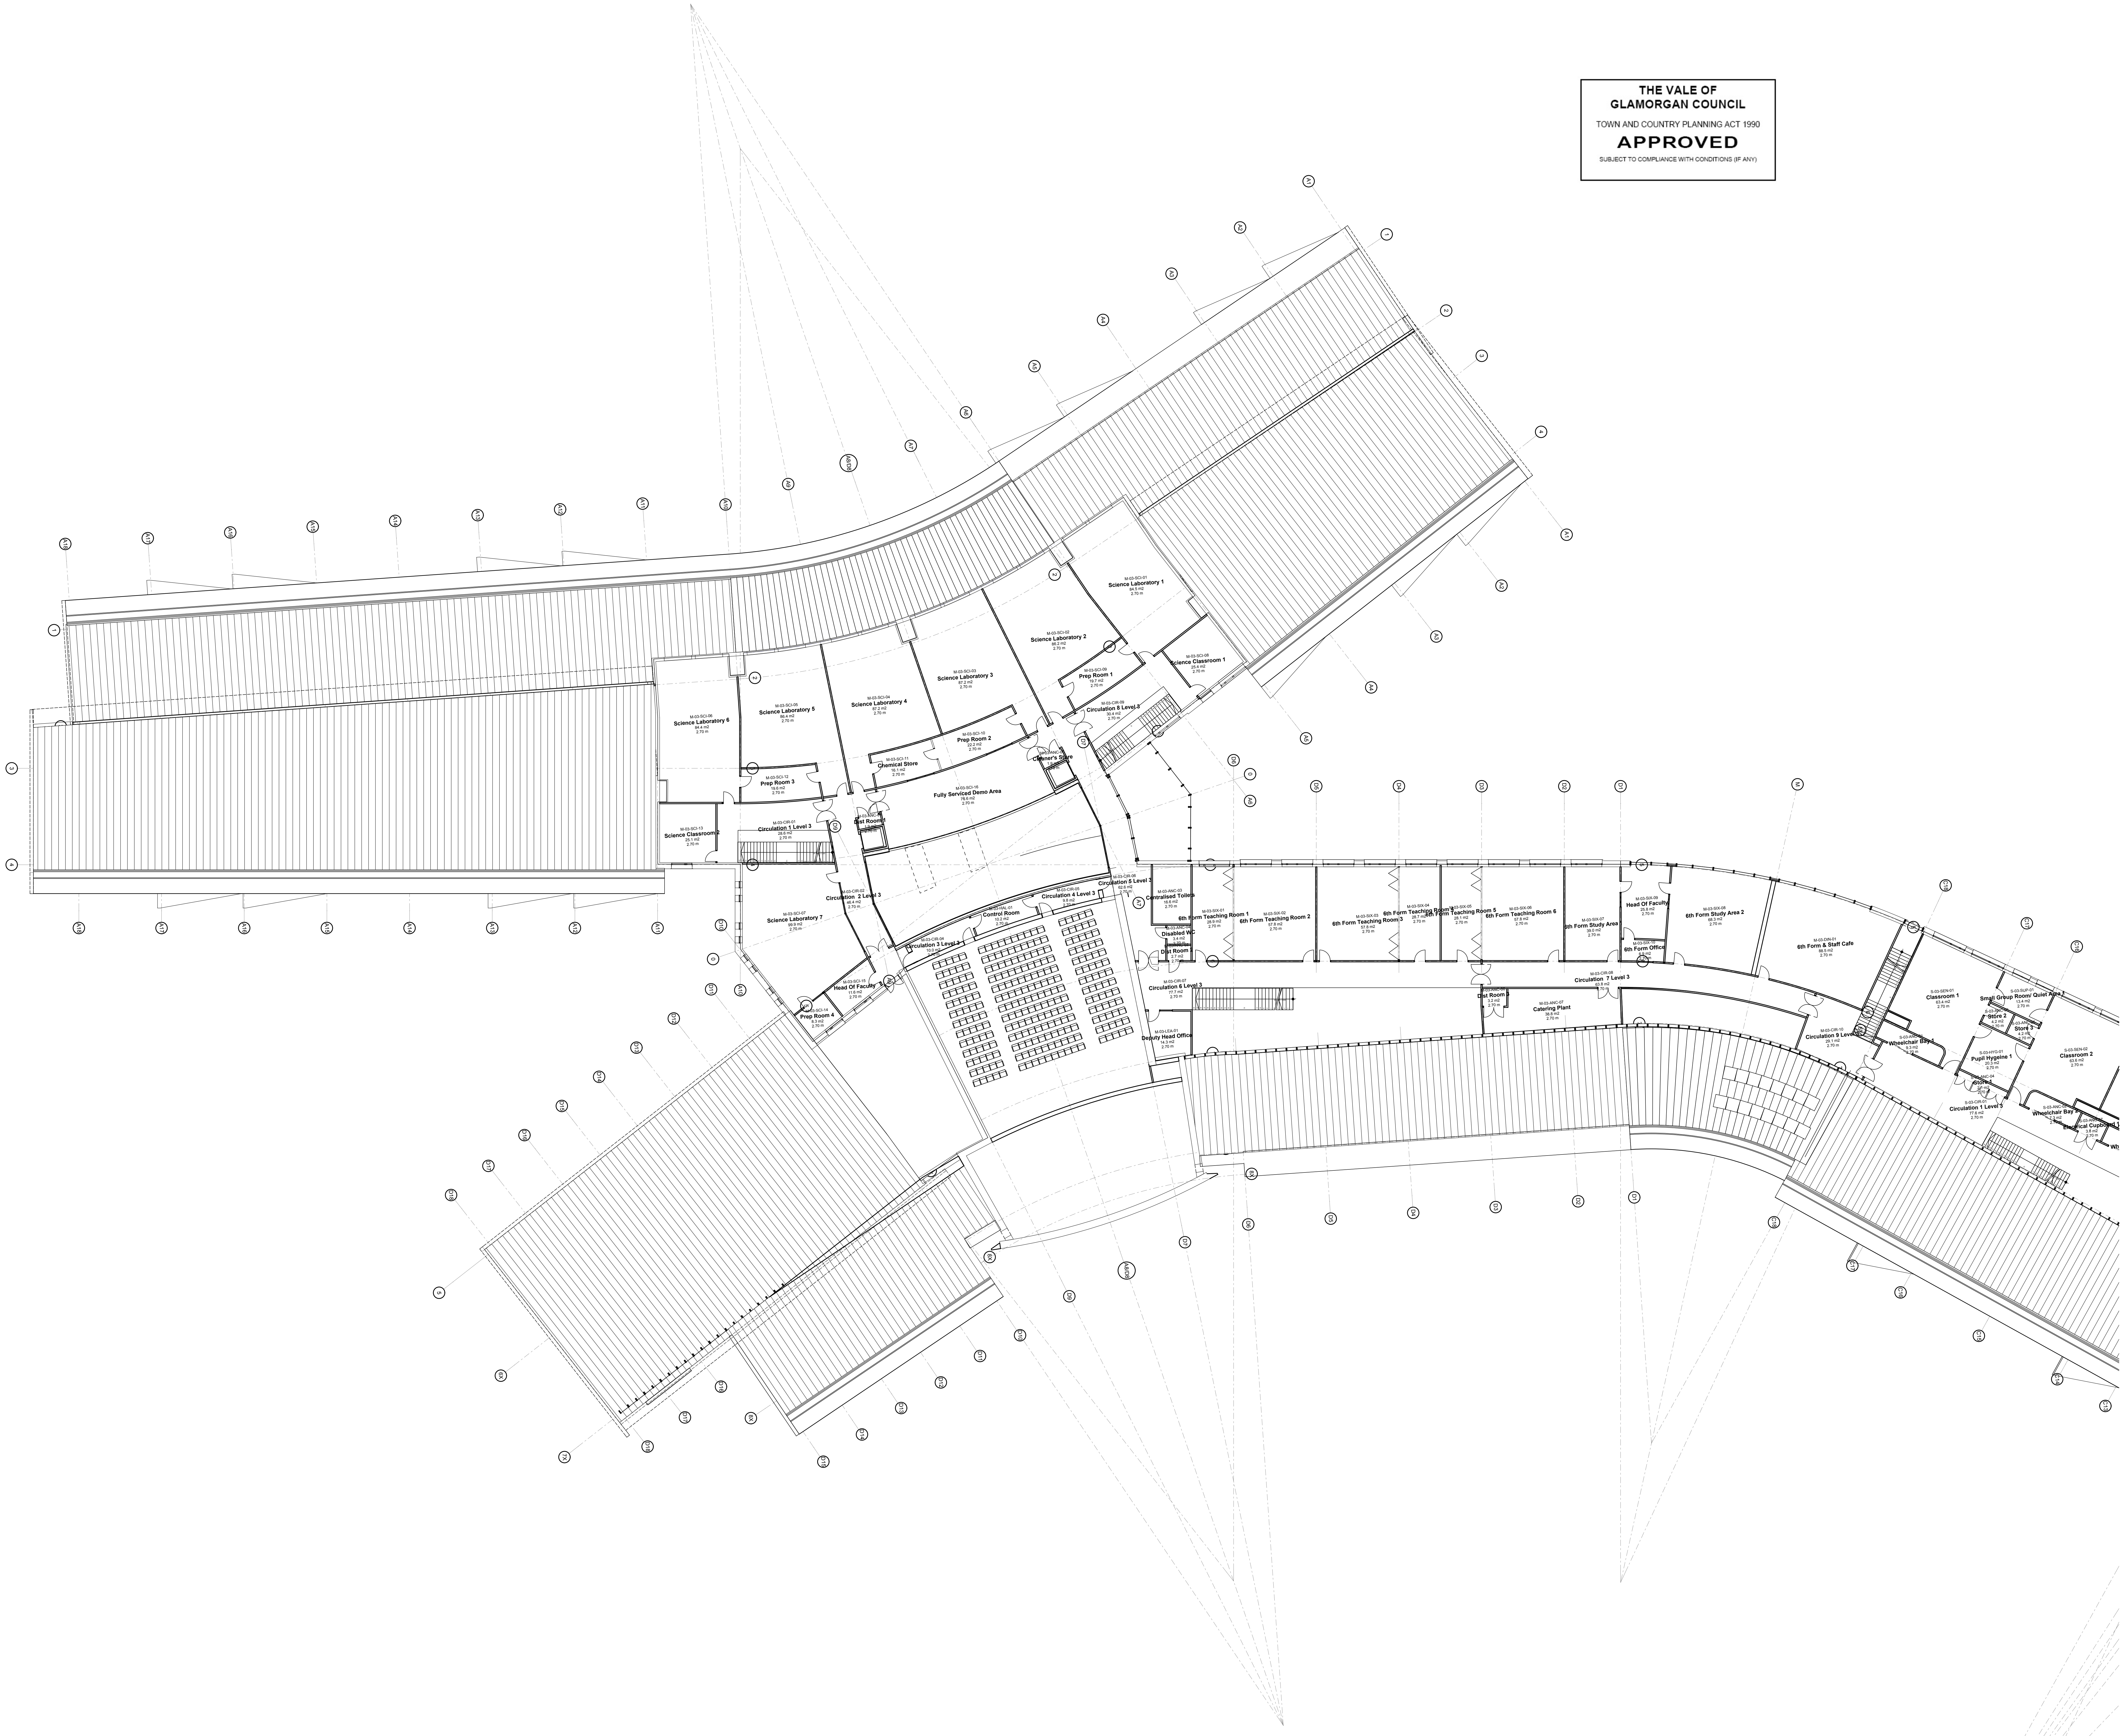
M-03-SCI-01 Science Laboratory 1 84.5 m2 2.70 m
M-03-SCI-02 Science Laboratory 2 86.2 m2 2.70 m
M-03-SCI-03 Science Laboratory 3 87.2 m2 2.70 m
M-03-SCI-04 Science Laboratory 4 87.2 m2 2.70 m
M-03-SCI-05 Science Laboratory 5 86.4 m2 2.70 m
M-03-SCI-06 Science Laboratory 6 84.4 m2 2.70 m
M-03-SCI-08 Science Classroom 1 25.4 m2 2.70 m
M-03-SCI-09 Prep Room 1 19.7 m2 2.70 m
M-03-CIR-09 Circulation 8 Level 3 30.4 m2 2.70 m
M-03-SCI-10 Prep Room 2 22.2 m2 2.70 m
M-03-SCI-11 Chemical Store 16.1 m2 2.70 m
M-03-ANC-0 Cleaner's Store 1.9 m2 2.70 m
M-03-SCI-12 Prep Room 3 19.6 m2 2.70 m
M-03-SCI-16 Fully Serviced Demo Area 76.6 m2 2.70 m
M-03-ANC-0 Dist Room 1 1.9 m2 2.70 m
M-03-SCI-13 Science Classroom 2 25.1 m2 2.70 m
M-03-CIR-01 Circulation 1 Level 3 28.6 m2 2.70 m
M-03-CIR-02 Circulation 2 Level 3 46.4 m2 2.70 m
M-03-SCI-07 Science Laboratory 7 99.9 m2 2.70 m
M-03-SCI-15 Head Of Faculty 11.6 m2 2.70 m
M-03-SCI-14 Prep Room 4 8.3 m2 2.70 m
M-03-CIR-06 Circulation 5 Level 3 62.6 m2 2.70 m
M-03-CIR-05 Circulation 4 Level 3 9.8 m2 2.70 m
M-03-HAL-01 Control Room 10.2 m2 2.70 m
M-03-CIR-04 Circulation 3 Level 3 10.0 m2 2.70 m
M-03-ANC-03 Centralised Toilets 16.6 m2 2.70 m
M-03-ANC-04 Disabled WC 3.4 m2 2.70 m
M-03-ANC-02 Dist Room 2 2.7 m2 2.70 m
M-03-CIR-07 Circulation 6 Level 3 77.7 m2 2.70 m
M-03-LEA-01 Deputy Head Office 14.3 m2 2.70 m
M-03-SIX-01 6th Form Teaching Room 1 28.9 m2 2.70 m
M-03-SIX-02 6th Form Teaching Room 2 57.8 m2 2.70 m
M-03-SIX-03 6th Form Teaching Room 3 57.8 m2 2.70 m
M-03-SIX-04 6th Form Teaching Room 4 28.7 m2 2.70 m
M-03-SIX-05 6th Form Teaching Room 5 28.1 m2 2.70 m
M-03-SIX-06 6th Form Teaching Room 6 57.8 m2 2.70 m
M-03-SIX-07 6th Form Study Area 39.0 m2 2.70 m
M-03-SIX-09 Head Of Faculty 25.8 m2 2.70 m
M-03-SIX-10 6th Form Office 6.9 m2 2.70 m
M-03-CIR-08 Circulation 7 Level 3 63.8 m2 2.70 m
M-03-ANC-06 Dist Room 3 3.2 m2 2.70 m
M-03-ANC-07 Catering Plant 38.8 m2 2.70 m
M-03-SIX-08 6th Form Study Area 2 68.3 m2 2.70 m
M-03-DIN-01 6th Form & Staff Cafe 88.5 m2 2.70 m
M-03-CIR-10 Circulation 9 Level 3 29.1 m2 2.70 m
S-03-SEN-01 Classroom 1 63.4 m2 2.70 m
S-03-SUP-01 Small Group Room/ Quiet Area 1 13.4 m2 2.70 m
S-03-ANC-05 Store 2 4.2 m2 2.70 m
S-03-ANC-06 Store 3 4.2 m2 2.70 m
S-03-ANC-01 Wheelchair Bay 1 9.3 m2 2.70 m
S-03-HYG-01 Pupil Hygeine 1 20.3 m2 2.70 m
S-03-ANC-04 Store 1 2.1 m2 2.70 m
S-03-CIR-01 Circulation 1 Level 3 77.6 m2 2.70 m
S-03-SEN-02 Classroom 2 63.6 m2 2.70 m
S-03-ANC-02 Wheelchair Bay 2 7.3 m2 2.70 m
S-03-ANC-07 Electrical Cupboard 1 3.8 m2 2.70 m
A6
A7
A9
A10
A11
A8/D8
D1
D2
D3
D4
D5
D6
D7
D9
D10
D11
D12
D13
C16
C17
C18
M

Notes

Check all dimensions on site. Do not scale from this drawing
Report any discrepancies and omissions to HLM Architects
This Drawing is Copyright ©

DESIGN/SKETCH DESIGN
Unless stated otherwise, the designs shown are subject to detailed site survey, investigations, and legal definition, the CDM Regulations, and the comments and / or approval of the various relevant Local Authority Officers, Statutory Undertakers, Fire Officers, Engineers and the like. They are copyright, project specific and confidential and no part is to be used or copied in any way without the express prior consent of HLM Architects.

PHOTOCOPIED/SCANNED INFORMATION
NB This drawing is based on photocopied / scanned information liable to distortion in scale.

AREA CALCULATIONS
NB The areas shown are approximate only and have been measured off preliminary drawings as the likely areas at the current state of design using the stated option from the Code of Measuring Practice, 4th edition. RICS / ISVA. These may be affected by future design development and construction tolerances, or the result of surveys for existing buildings. Take account of these factors before planning any financial or property development purpose or strategy and seek confirmation of latest areas before decision making.

3RD-PARTY INFORMATION
NB This drawing includes information provided by independent surveyors and / or consultants, to whom all queries shall be made. HLM Architects can accept no liability for its content or accuracy.

Rev Description	Date	Drn	Chk
Issued for Planning	04/04/12	MR	PG

Project

PENARTH LEARNING COMMUNITY

Client

Title

MAINSTREAM SCHOOL LEVEL 3 FLOOR PLAN

Drawing No.	Revision
08013 / 1L(05)003	PA1

Scale @ A0	Drawn
1:200	MLL
Date	**Checked**
05/01/2012	HLM

HLM
2nd Floor, Greyfriars House,
Greyfriars Road,
Cardiff, CF10 3AL
T: +44 (0)29 2039 6070
F: +44 (0)29 2039 6080
E: cardiff@hlmarchitects.com
Architecture
Landscape & Urban Design
Interiors
Environment
www.hlmarchitects.com
LONDON SHEFFIELD GLASGOW BELFAST **CARDIFF** PLYMOUTH ABU DHABI SOUTH AFRICA