Notes

Check all dimensions on site. Do not scale from this drawing
Report any discrepancies and omissions to HLM Architects
This Drawing is Copyright ©

DESIGN/SKETCH DESIGN
Unless stated otherwise, the designs shown are subject to detailed site survey, investigations, and legal definition, the CDM Regulations, and the comments and / or approval of the various relevant Local Authority Officers, Statutory Undertakers, Fire Officers, Engineers and the like. They are copyright, project specific and confidential and no part is to be used or copied in any way without the express prior consent of HLM Architects.

PHOTOCOPIED/SCANNED INFORMATION
NB This drawing is based on photocopied / scanned information liable to distortion in scale.

AREA CALCULATIONS
NB The areas shown are approximate only and have been measured off preliminary drawings as the likely areas at the current state of design using the stated option from the Code of Measuring Practice, 4th edition. RICS / ISVA. These may be affected by future design development and construction tolerances, or the result of surveys for existing buildings. Take account of these factors before planning any financial or property development purpose or strategy and seek confirmation of latest areas before decision making.

3RD-PARTY INFORMATION
NB This drawing includes information provided by independent surveyors and / or consultants, to whom all queries shall be made. HLM Architects can accept no liability for its content or accuracy.

THE VALE OF
GLAMORGAN COUNCIL
TOWN AND COUNTRY PLANNING ACT 1990
APPROVED
SUBJECT TO COMPLIANCE WITH CONDITIONS (IF ANY)

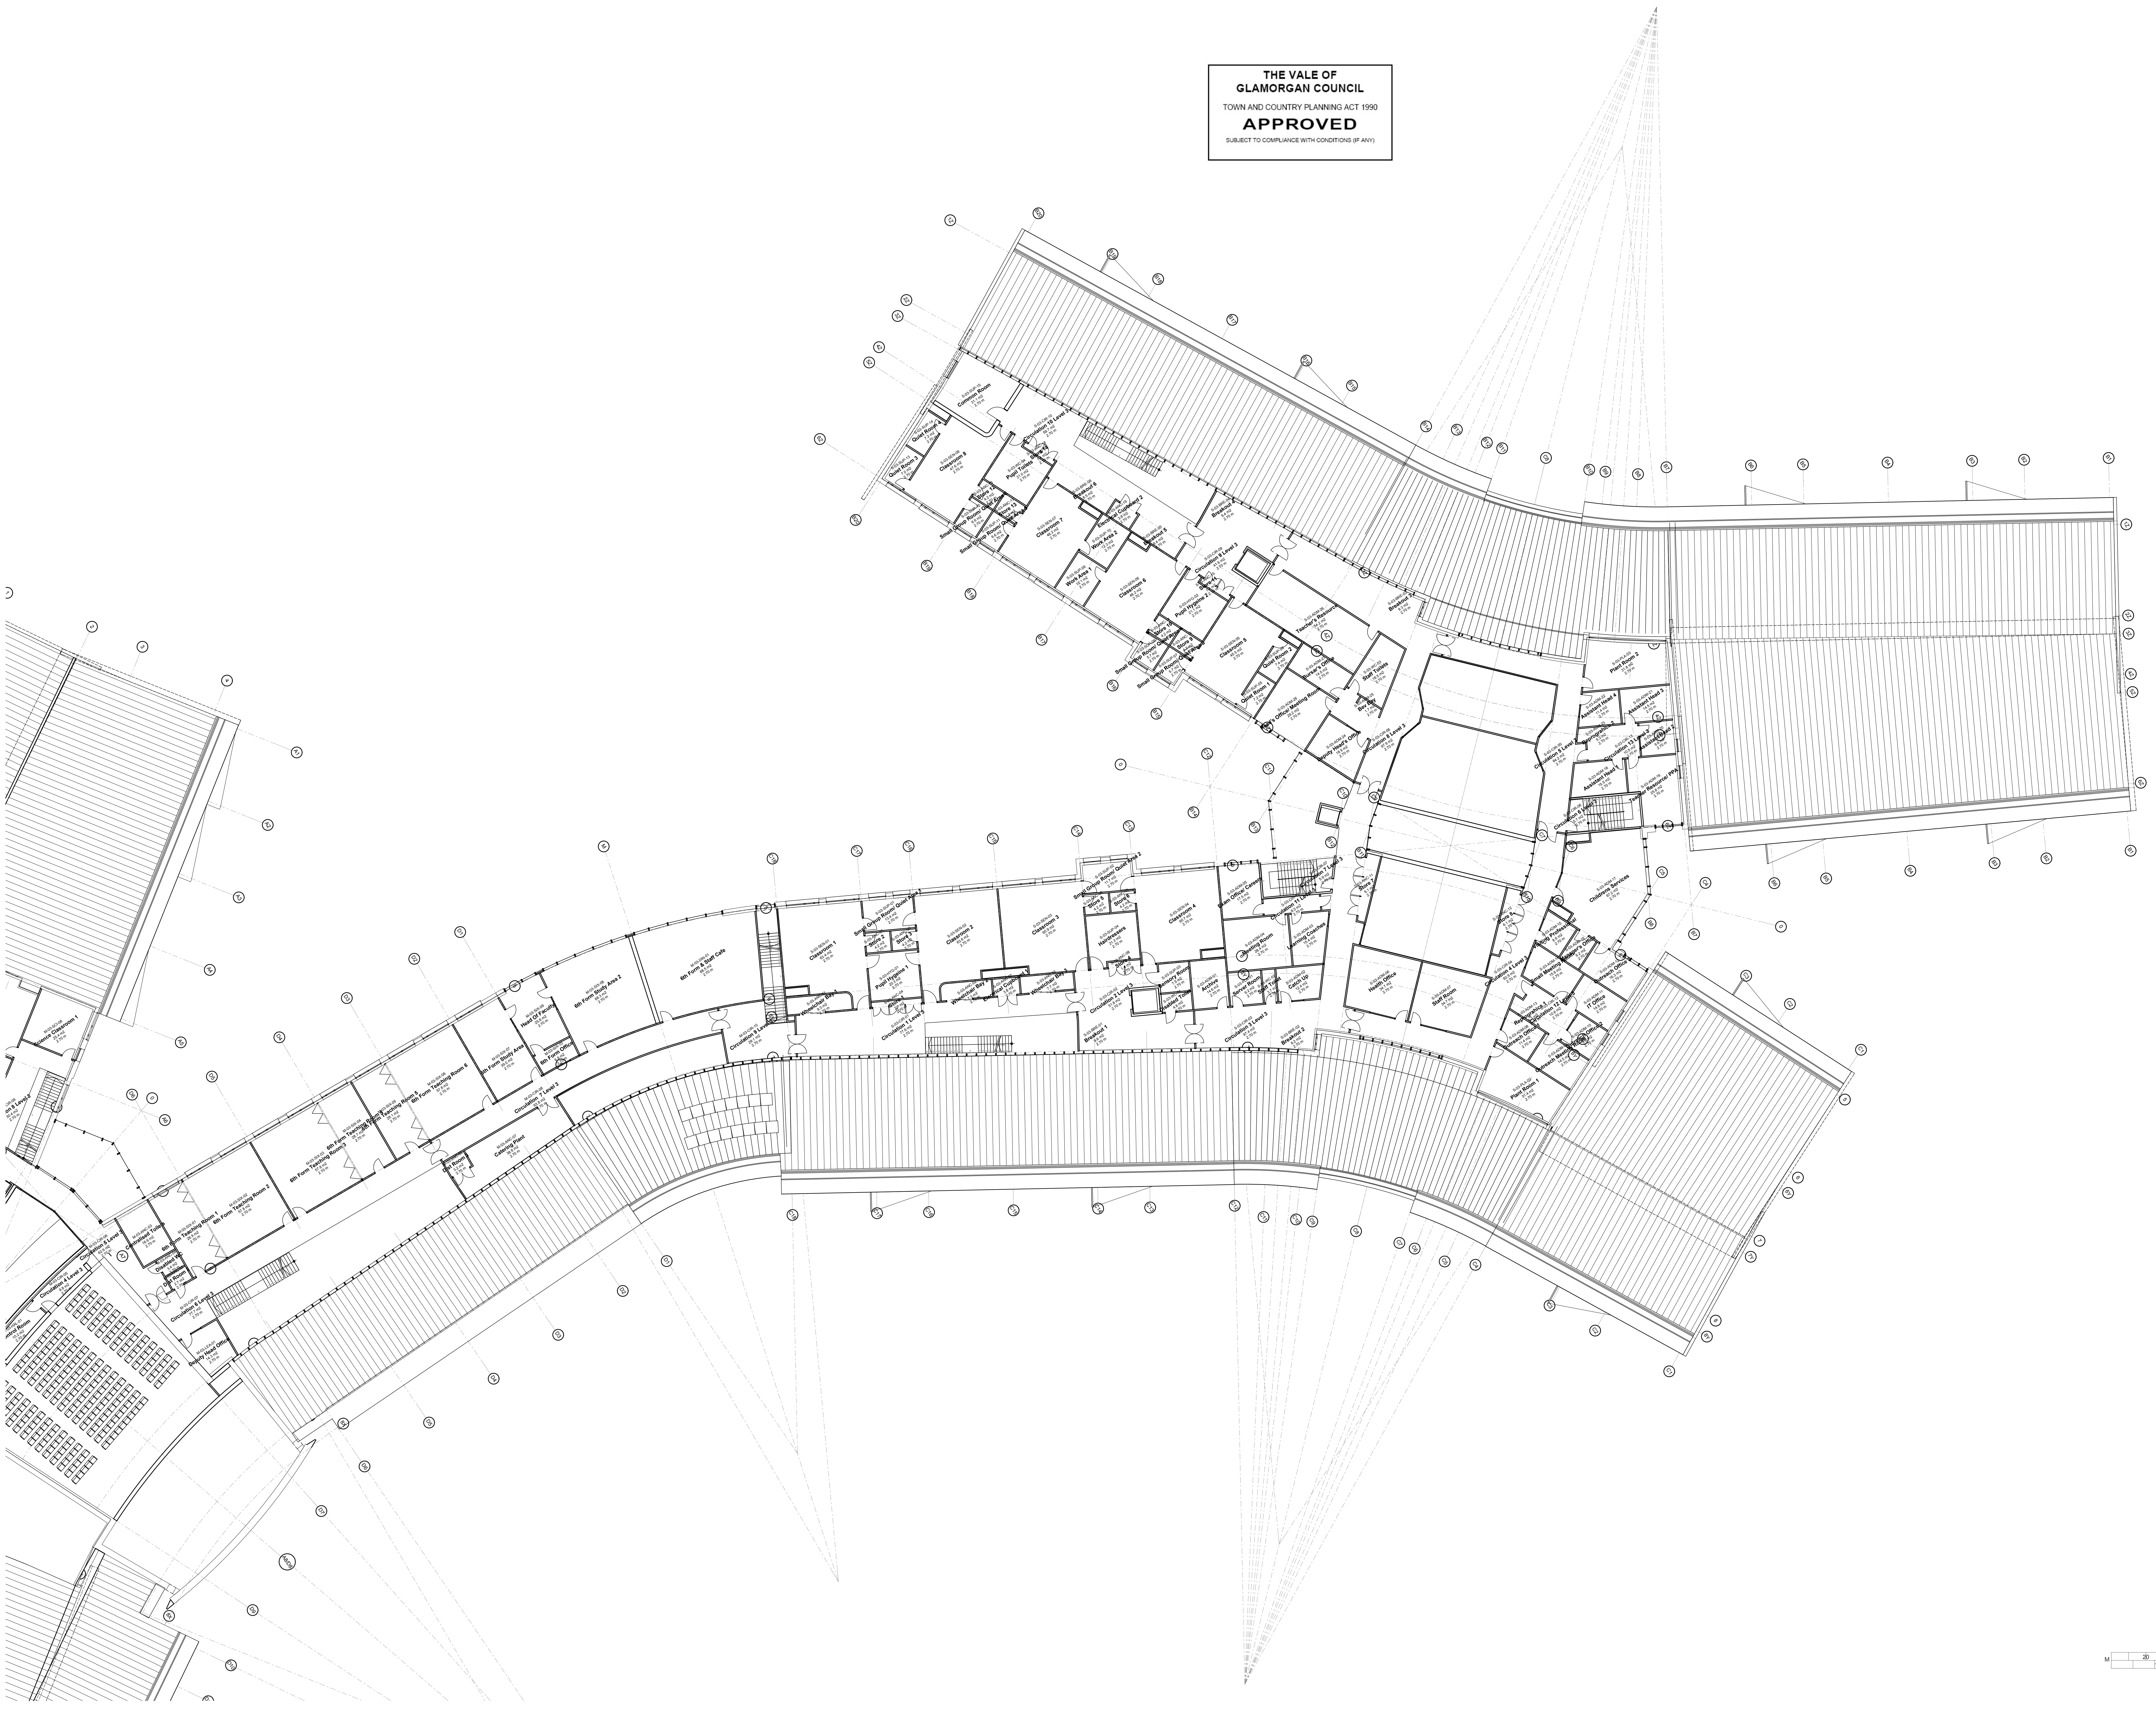

Rev Description	Date	Drn	Chk
Issued for Planning	04/04/12	MR	PG

Project

PENARTH LEARNING COMMUNITY

Client

Title

SEN SCHOOL LEVEL 3 FLOOR PLAN

Drawing No. | Revision
08013 / 2L(05)003 | PA1

Scale @ A0: 1:200
Drawn: MLL
Date: 05/01/2012
Checked: HLM

HLM

2nd Floor, Greyfriars House,
Greyfriars Road,
Cardiff, CF10 3AL
T: +44 (0)29 2039 6070
F: +44 (0)29 2039 6080
E: cardiff@hlmarchitects.com

Architecture
Landscape & Urban Design
Interiors
Environment

www.hlmarchitects.com

LONDON SHEFFIELD GLASGOW BELFAST **CARDIFF** PLYMOUTH ABU DHABI SOUTH AFRICA