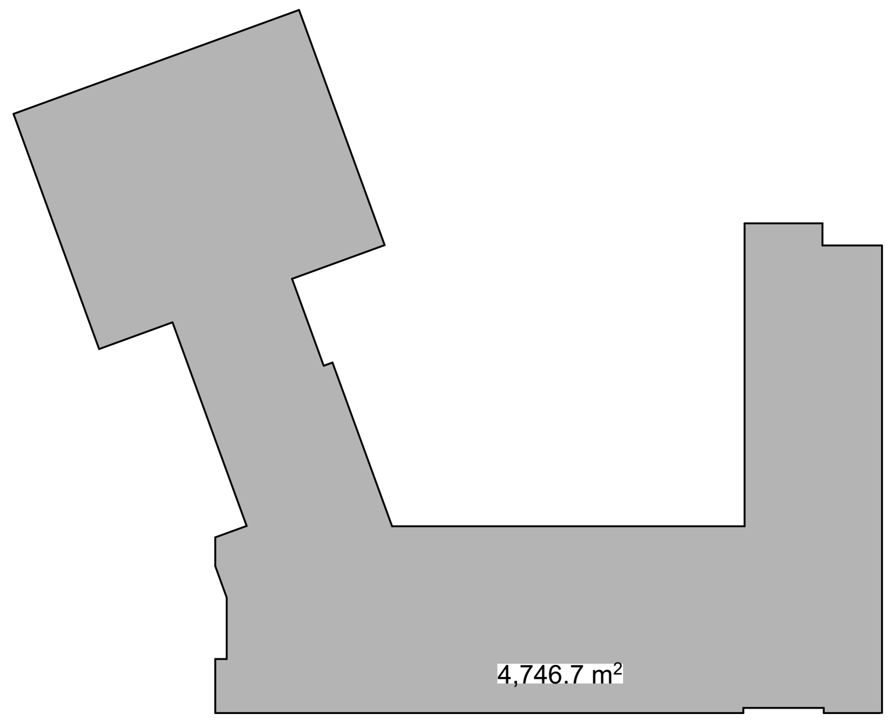

GIFA

Ground Floor: 4746.7 m^2

1st Floor: 2938.8 m^2

2nd Floor: 3361.9 m^2

Total GIFA: 11047.4 m^2

Proposed Expansion Zone: 393.2 m^2

Plant Area: 75.3 m^2

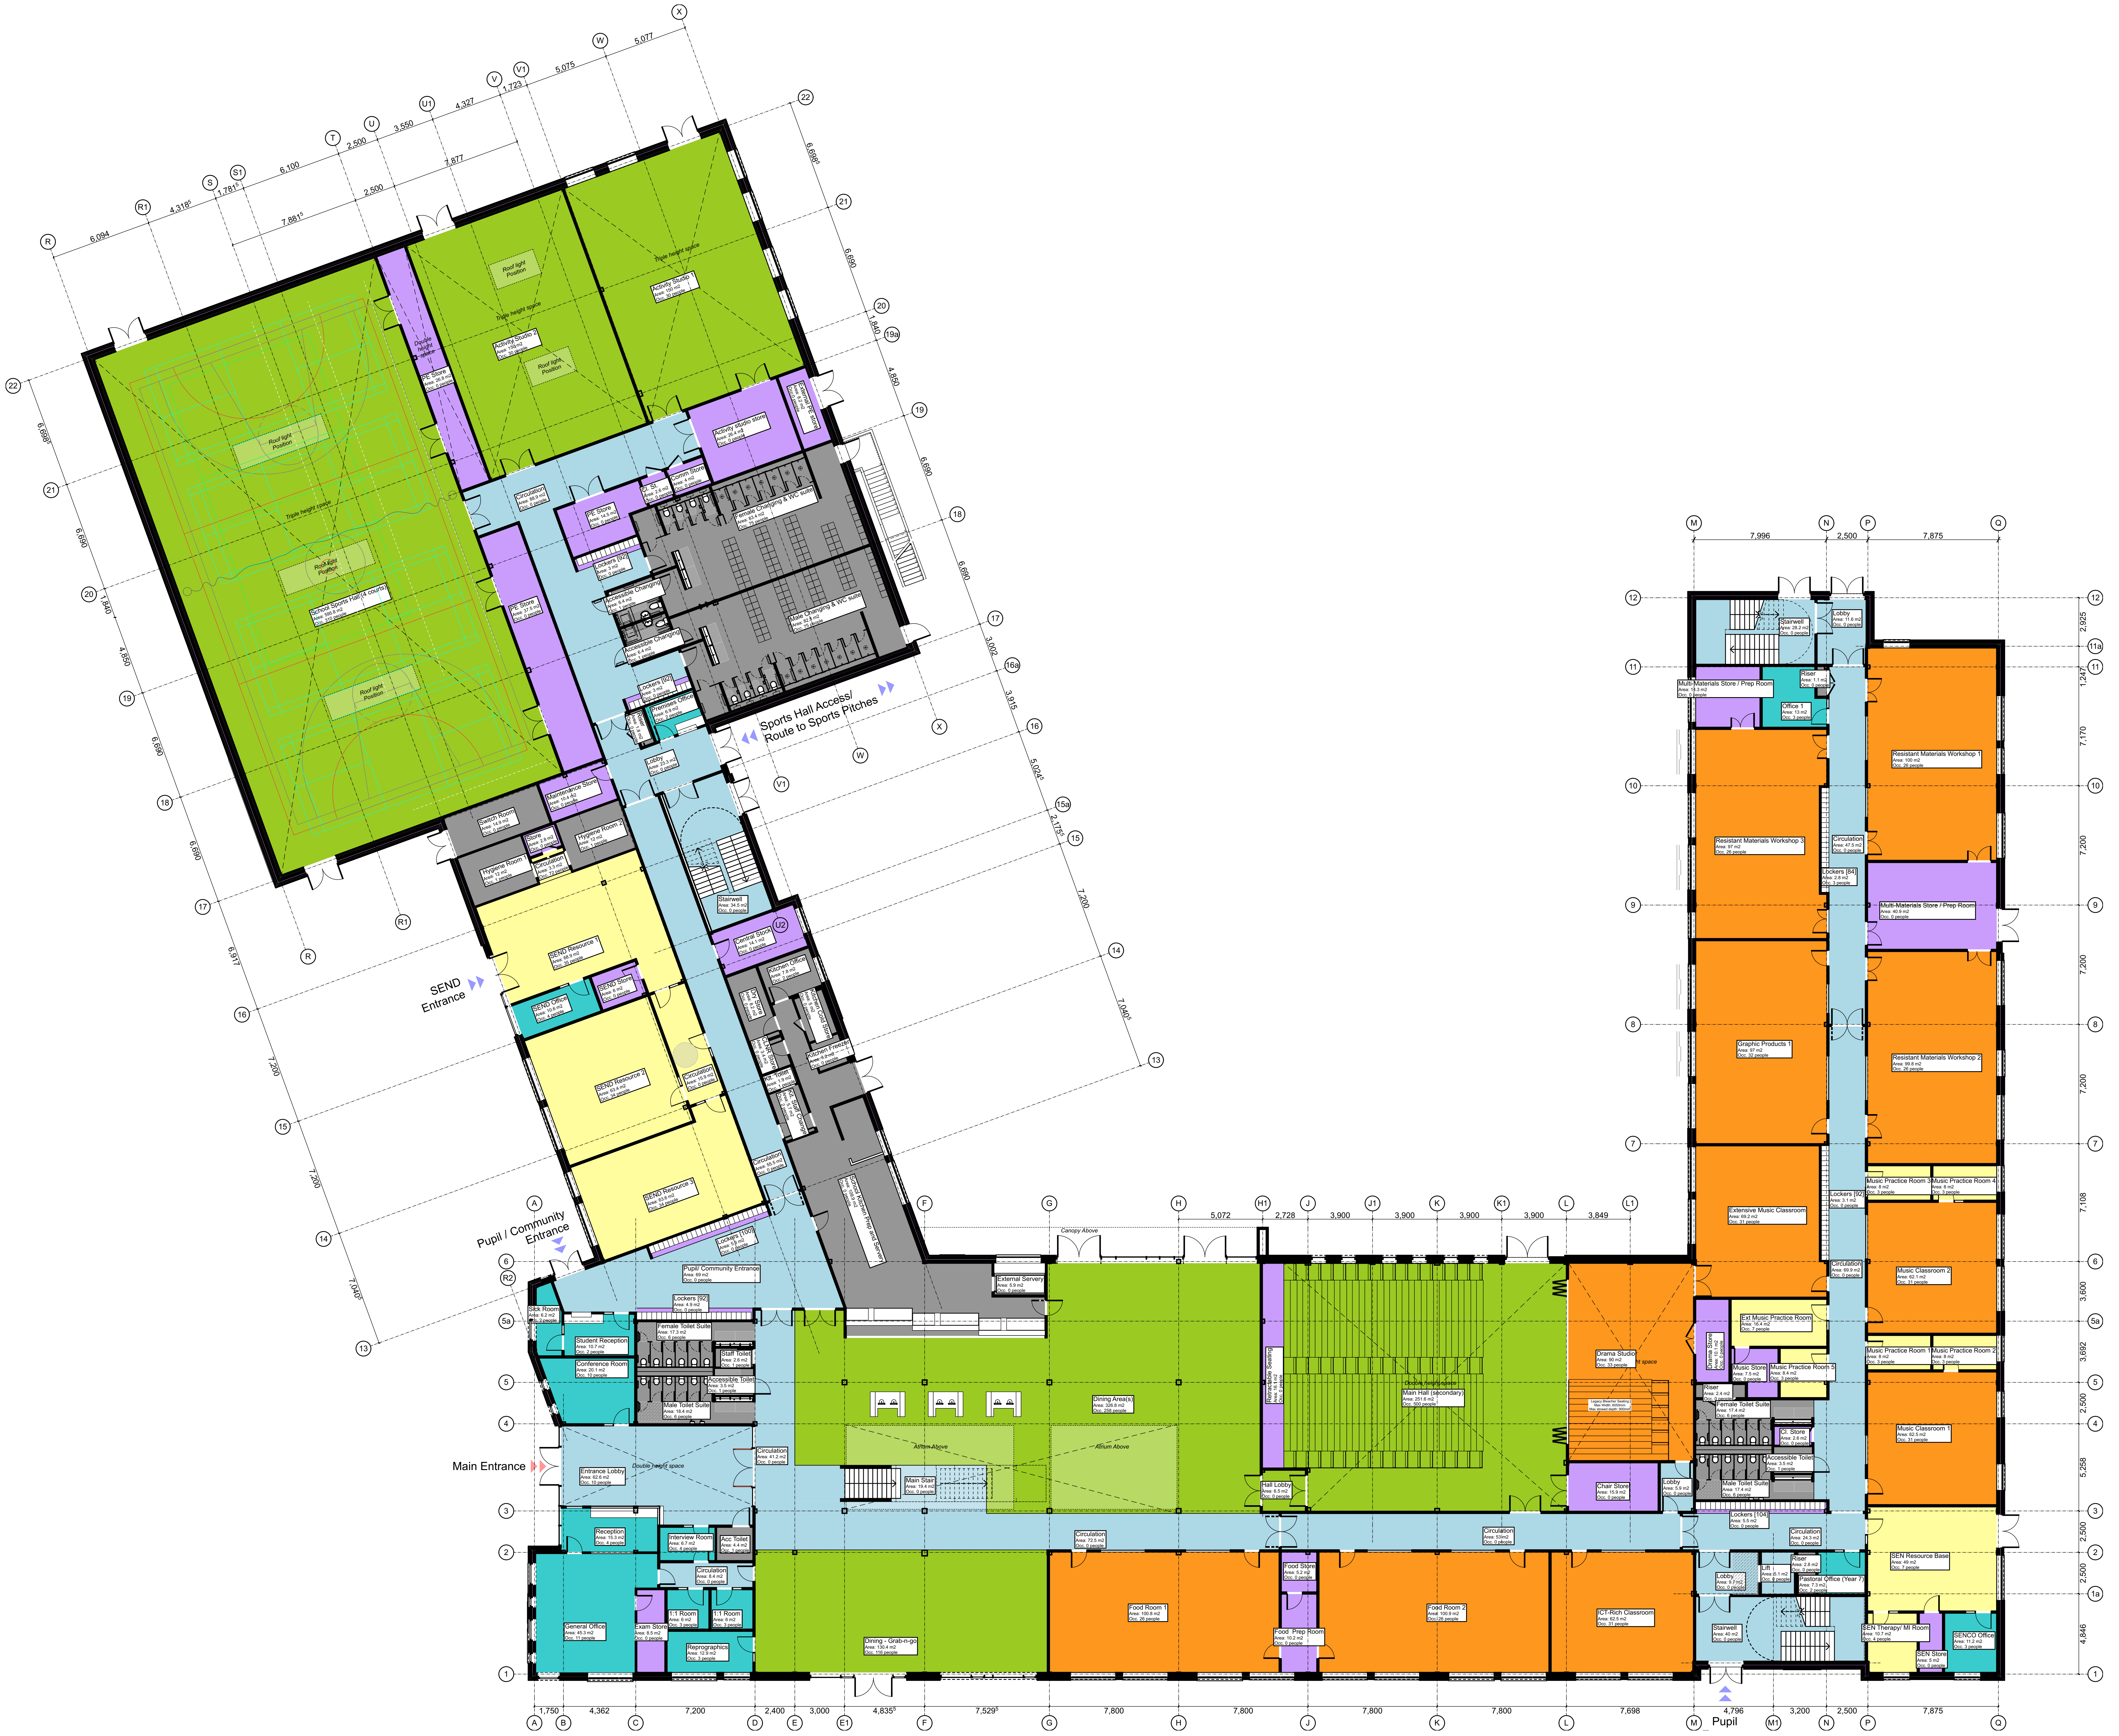

rev	description	drawn	checked	date
P01	First issue	RR	AM	13.02.2020

B O N D B R Y A N

The Church Studio Springvale Road Sheffield S10 1LP

t +44(0)114 266 2040 w www.bondbryan.com
e BPTC@bondbryan.co.uk

Benton Park School
Harrogate Road, Rawdon, Leeds, LS19 6LX

BAM Construction

bam

GROUND FLOOR GA PLAN

bba project ref	scale(s)	original paper size
16-157A	1:200	A1

name :

project	originator	volume	level	type	role	number
BPS	**- BBA**	**- ZZ**	**- 00**	**- DR**	**- A**	**- 2001**

status : suitability description :
S2 **SUITABLE FOR INFORMATION**

revision : revision description :
P01 **PRELIMINARY**

This document is © Bond Bryan Architects Ltd. If in doubt ASK. Drawing measurements shall not be obtained by scaling. Verify all dimensions prior to construction. Immediately report any discrepancies on this document to the Architect. This document shall be read in conjunction with associated models, specifications and related consultant's documents.