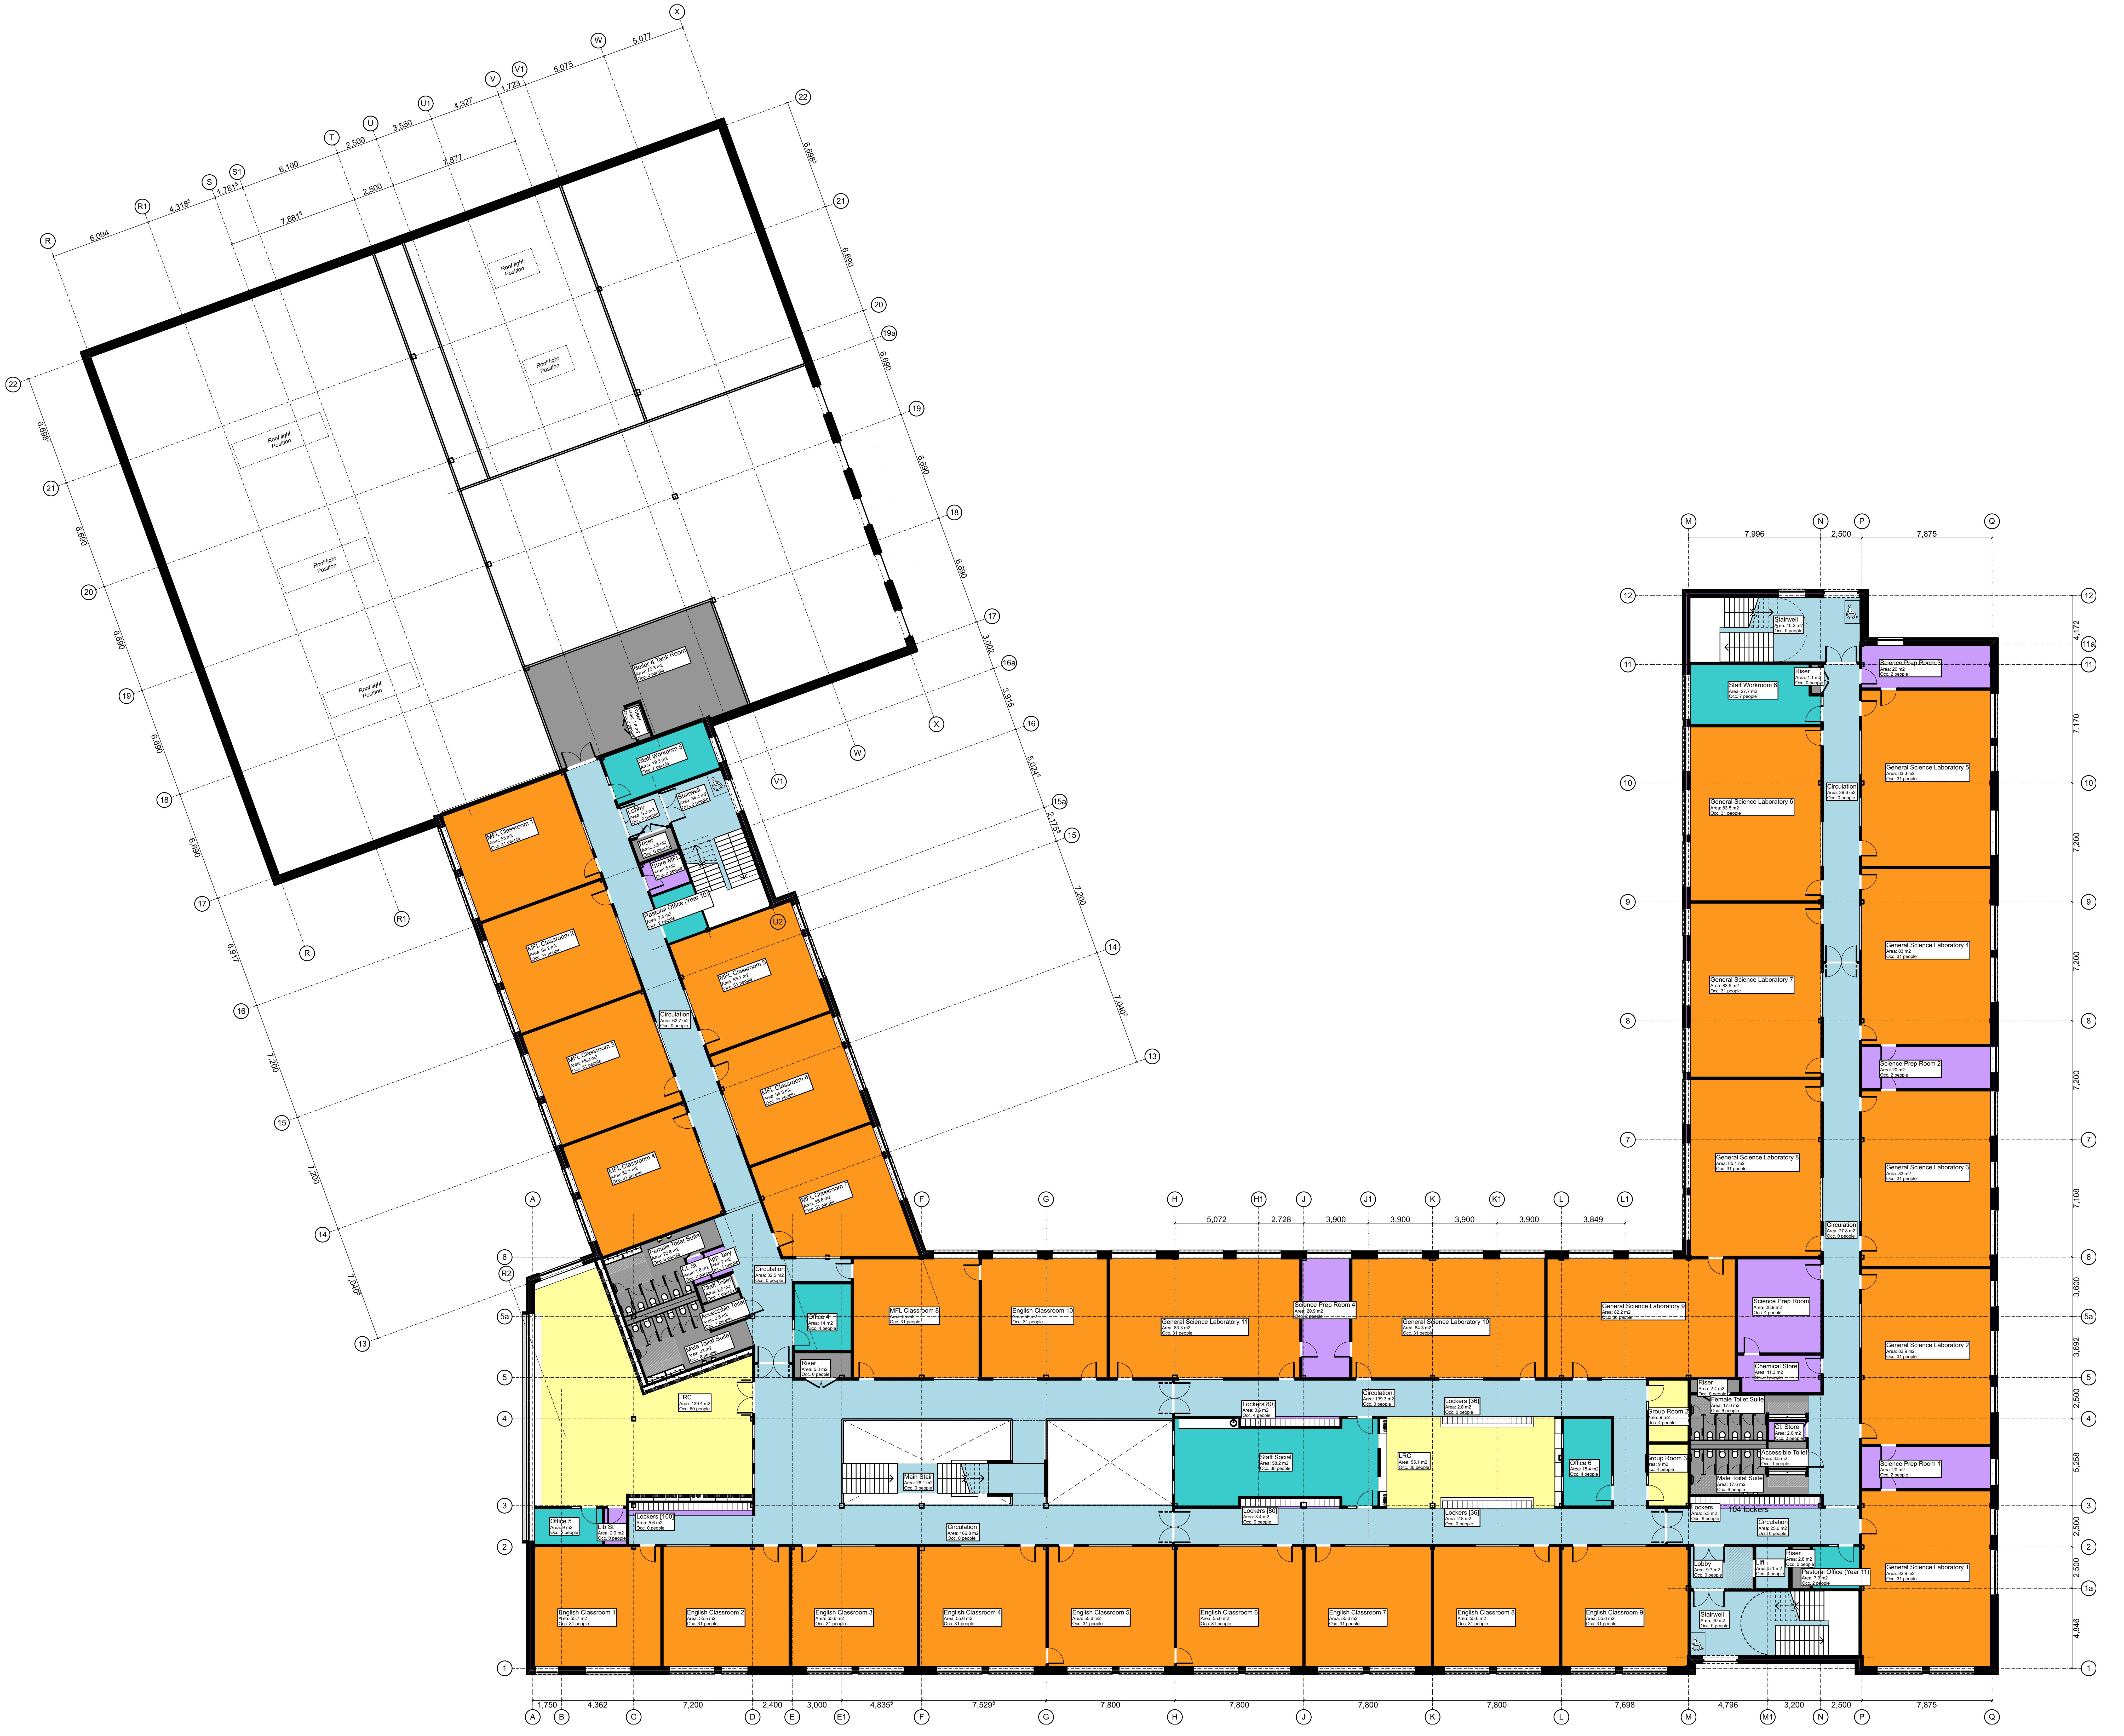
Roof light Position
Roof light Position
Roof light Position
Roof light Position
Roof light Position
Boiler & Tank Room Area: 75.3 m2 Occ. 0 people
Riser Area: 1.8 m2 Occ. 0 people
Staff Workroom 5 Area: 19.5 m2 Occ. 7 people
Lobby Area: 5.3 m2 Occ. 0 people
Stairwell Area: 34.4 m2 Occ. 0 people
Riser Area: 3.5 m2 Occ. 0 people
Store MFL Area: 5 m2 Occ. 0 people
Pastoral Office (Year 10) Area: 7.4 m2 Occ. 2 people
MFL Classroom 1 Area: 53 m2 Occ. 31 people
MFL Classroom 2 Area: 55.2 m2 Occ. 31 people
MFL Classroom 3 Area: 55.2 m2 Occ. 31 people
MFL Classroom 4 Area: 55.1 m2 Occ. 31 people
MFL Classroom 5 Area: 55.1 m2 Occ. 31 people
MFL Classroom 6 Area: 54.8 m2 Occ. 31 people
MFL Classroom 7 Area: 55.8 m2 Occ. 31 people
Circulation Area: 62.7 m2 Occ. 0 people
Female Toilet Suite Area: 22.6 m2 Occ. 6 people
Cl. St Area: 1.6 m2 Occ. 0 people
App. bay Area: 2 m2 Occ. 1 people
Staff Toilet Area: 2.6 m2 Occ. 1 people
Accessible Toilet Area: 3.5 m2 Occ. 1 people
Male Toilet Suite Area: 22 m2 Occ. 6 people
Circulation Area: 32.5 m2 Occ. 0 people
Office 4 Area: 14 m2 Occ. 4 people
Riser Area: 5.3 m2 Occ. 0 people
LRC Area: 139.4 m2 Occ. 60 people
Office 5 Area: 9 m2 Occ. 2 people
Lib St Area: 2.9 m2 Occ. 0 people
Lockers [100] Area: 5.6 m2 Occ. 0 people
MFL Classroom 8 Area: 55 m2 Occ. 31 people
English Classroom 10 Area: 55 m2 Occ. 31 people
General Science Laboratory 11 Area: 83.3 m2 Occ. 31 people
Science Prep Room 4 Area: 20.9 m2 Occ. 2 people
General Science Laboratory 10 Area: 84.3 m2 Occ. 31 people
General Science Laboratory 9 Area: 82.2 m2 Occ. 30 people
Main Stair Area: 28.1 m2 Occ. 0 people
Circulation Area: 166.8 m2 Occ. 0 people
Lockers[80] Area: 3.6 m2 Occ. 4 people
Staff Social Area: 58.2 m2 Occ. 38 people
Lockers [80] Area: 3.4 m2 Occ. 0 people
Circulation Area: 139.3 m2 Occ. 0 people
Lockers [36] Area: 2.8 m2 Occ. 0 people
LRC Area: 55.1 m2 Occ. 30 people
Lockers [36] Area: 2.8 m2 Occ. 0 people
Office 6 Area: 15.4 m2 Occ. 4 people
Group Room 2 Area: 9 m2 Occ. 4 people
Group Room 3 Area: 9 m2 Occ. 4 people
Riser Area: 2.4 m2 Occ. 0 people
Female Toilet Suite Area: 17.6 m2 Occ. 6 people
Cl. Store Area: 2.6 m2 Occ. 0 people
Accessible Toilet Area: 3.5 m2 Occ. 1 people
Male Toilet Suite Area: 17.6 m2 Occ. 6 people
Lockers Area: 5.5 m2 Occ. 6 people
104 lockers
Circulation Area: 25.6 m2 Occ. 0 people
Science Prep Room Area: 28.9 m2 Occ. 4 people
Chemical Store Area: 11.3 m2 Occ. 0 people
Lobby Area: 9.7 m2 Occ. 0 people
Lift Area: 5.1 m2 Occ. 0 people
Riser Area: 2.8 m2 Occ. 0 people
Pastoral Office (Year 11) Area: 7.3 m2 Occ. 2 people
Stairwell Area: 40 m2 Occ. 0 people
English Classroom 1 Area: 55.7 m2 Occ. 31 people
English Classroom 2 Area: 55.5 m2 Occ. 31 people
English Classroom 3 Area: 55.6 m2 Occ. 31 people
English Classroom 4 Area: 55.6 m2 Occ. 31 people
English Classroom 5 Area: 55.6 m2 Occ. 31 people
English Classroom 6 Area: 55.6 m2 Occ. 31 people
English Classroom 7 Area: 55.6 m2 Occ. 31 people
English Classroom 8 Area: 55.6 m2 Occ. 31 people
English Classroom 9 Area: 55.6 m2 Occ. 31 people
Stairwell Area: 40.2 m2 Occ. 0 people
Riser Area: 1.1 m2 Occ. 0 people
Staff Workroom 6 Area: 27.7 m2 Occ. 7 people
Science Prep Room 3 Area: 20 m2 Occ. 2 people
General Science Laboratory 5 Area: 83.3 m2 Occ. 31 people
Circulation Area: 39.6 m2 Occ. 0 people
General Science Laboratory 6 Area: 83.5 m2 Occ. 31 people
General Science Laboratory 4 Area: 83 m2 Occ. 31 people
General Science Laboratory 7 Area: 83.5 m2 Occ. 31 people
Science Prep Room 2 Area: 20 m2 Occ. 2 people
General Science Laboratory 8 Area: 85.1 m2 Occ. 31 people
General Science Laboratory 3 Area: 83 m2 Occ. 31 people
Circulation Area: 77.8 m2 Occ. 0 people
General Science Laboratory 2 Area: 82.9 m2 Occ. 31 people
Science Prep Room 1 Area: 20 m2 Occ. 2 people
General Science Laboratory 1 Area: 82.9 m2 Occ. 31 people
7,996
2,500
7,875
5,072
2,728
3,900
3,900
3,900
3,900
3,849
1,750
4,362
7,200
2,400
3,000
4,835
7,529
7,800
7,800
7,800
7,800
7,698
4,796
3,200
2,500
7,875

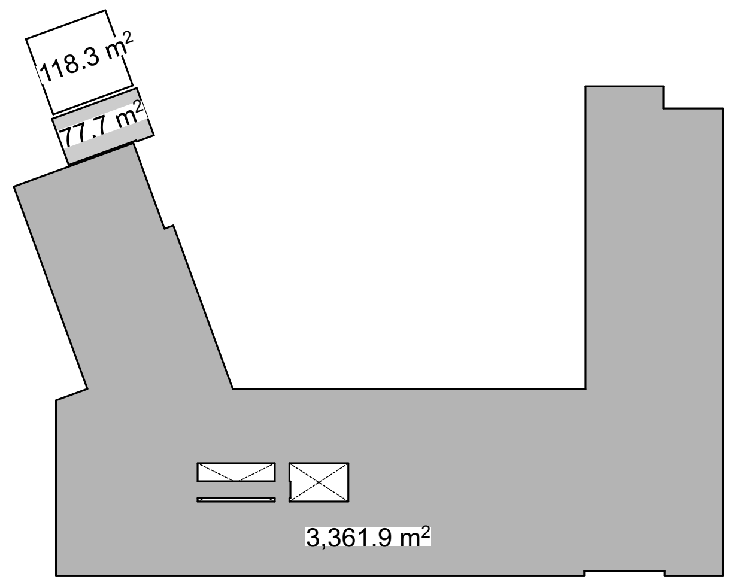

GIFA

Ground Floor: 4746.7 m²

1st Floor: 2938.8 m²

2nd Floor: 3361.9 m²

Total GIFA: 11047.4 m²

Proposed Expansion Zone: 393.2 m²

Plant Area: 75.3 m²

rev	description	drawn	checked	date
P01	First issue	RR	AM	13.02.2020

BOND BRYAN

The Church Studio Springvale Road Sheffield S10 1LP

t +44(0)114 266 2040 w www.bondbryan.com
e BPTC@bondbryan.co.uk

Benton Park School
Harrogate Road, Rawdon, Leeds, LS19 6LX

BAM Construction

bam

SECOND FLOOR GA PLAN

bba project ref	scale(s)	original paper size
16-157A	1:200	A1

name :

project	originator	volume	level	type	role	number
BPS	**BBA**	**ZZ**	**02**	**DR**	**A**	**2001**

status : suitability description :
S2 **SUITABLE FOR INFORMATION**
revision : revision description :
P01 **PRELIMINARY**

This document is © Bond Bryan Architects Ltd. If in doubt ASK. Drawing measurements shall not be obtained by scaling. Verify all dimensions prior to construction. Immediately report any discrepancies on this document to the Architect. This document shall be read in conjunction with associated models, specifications and related consultant's documents.