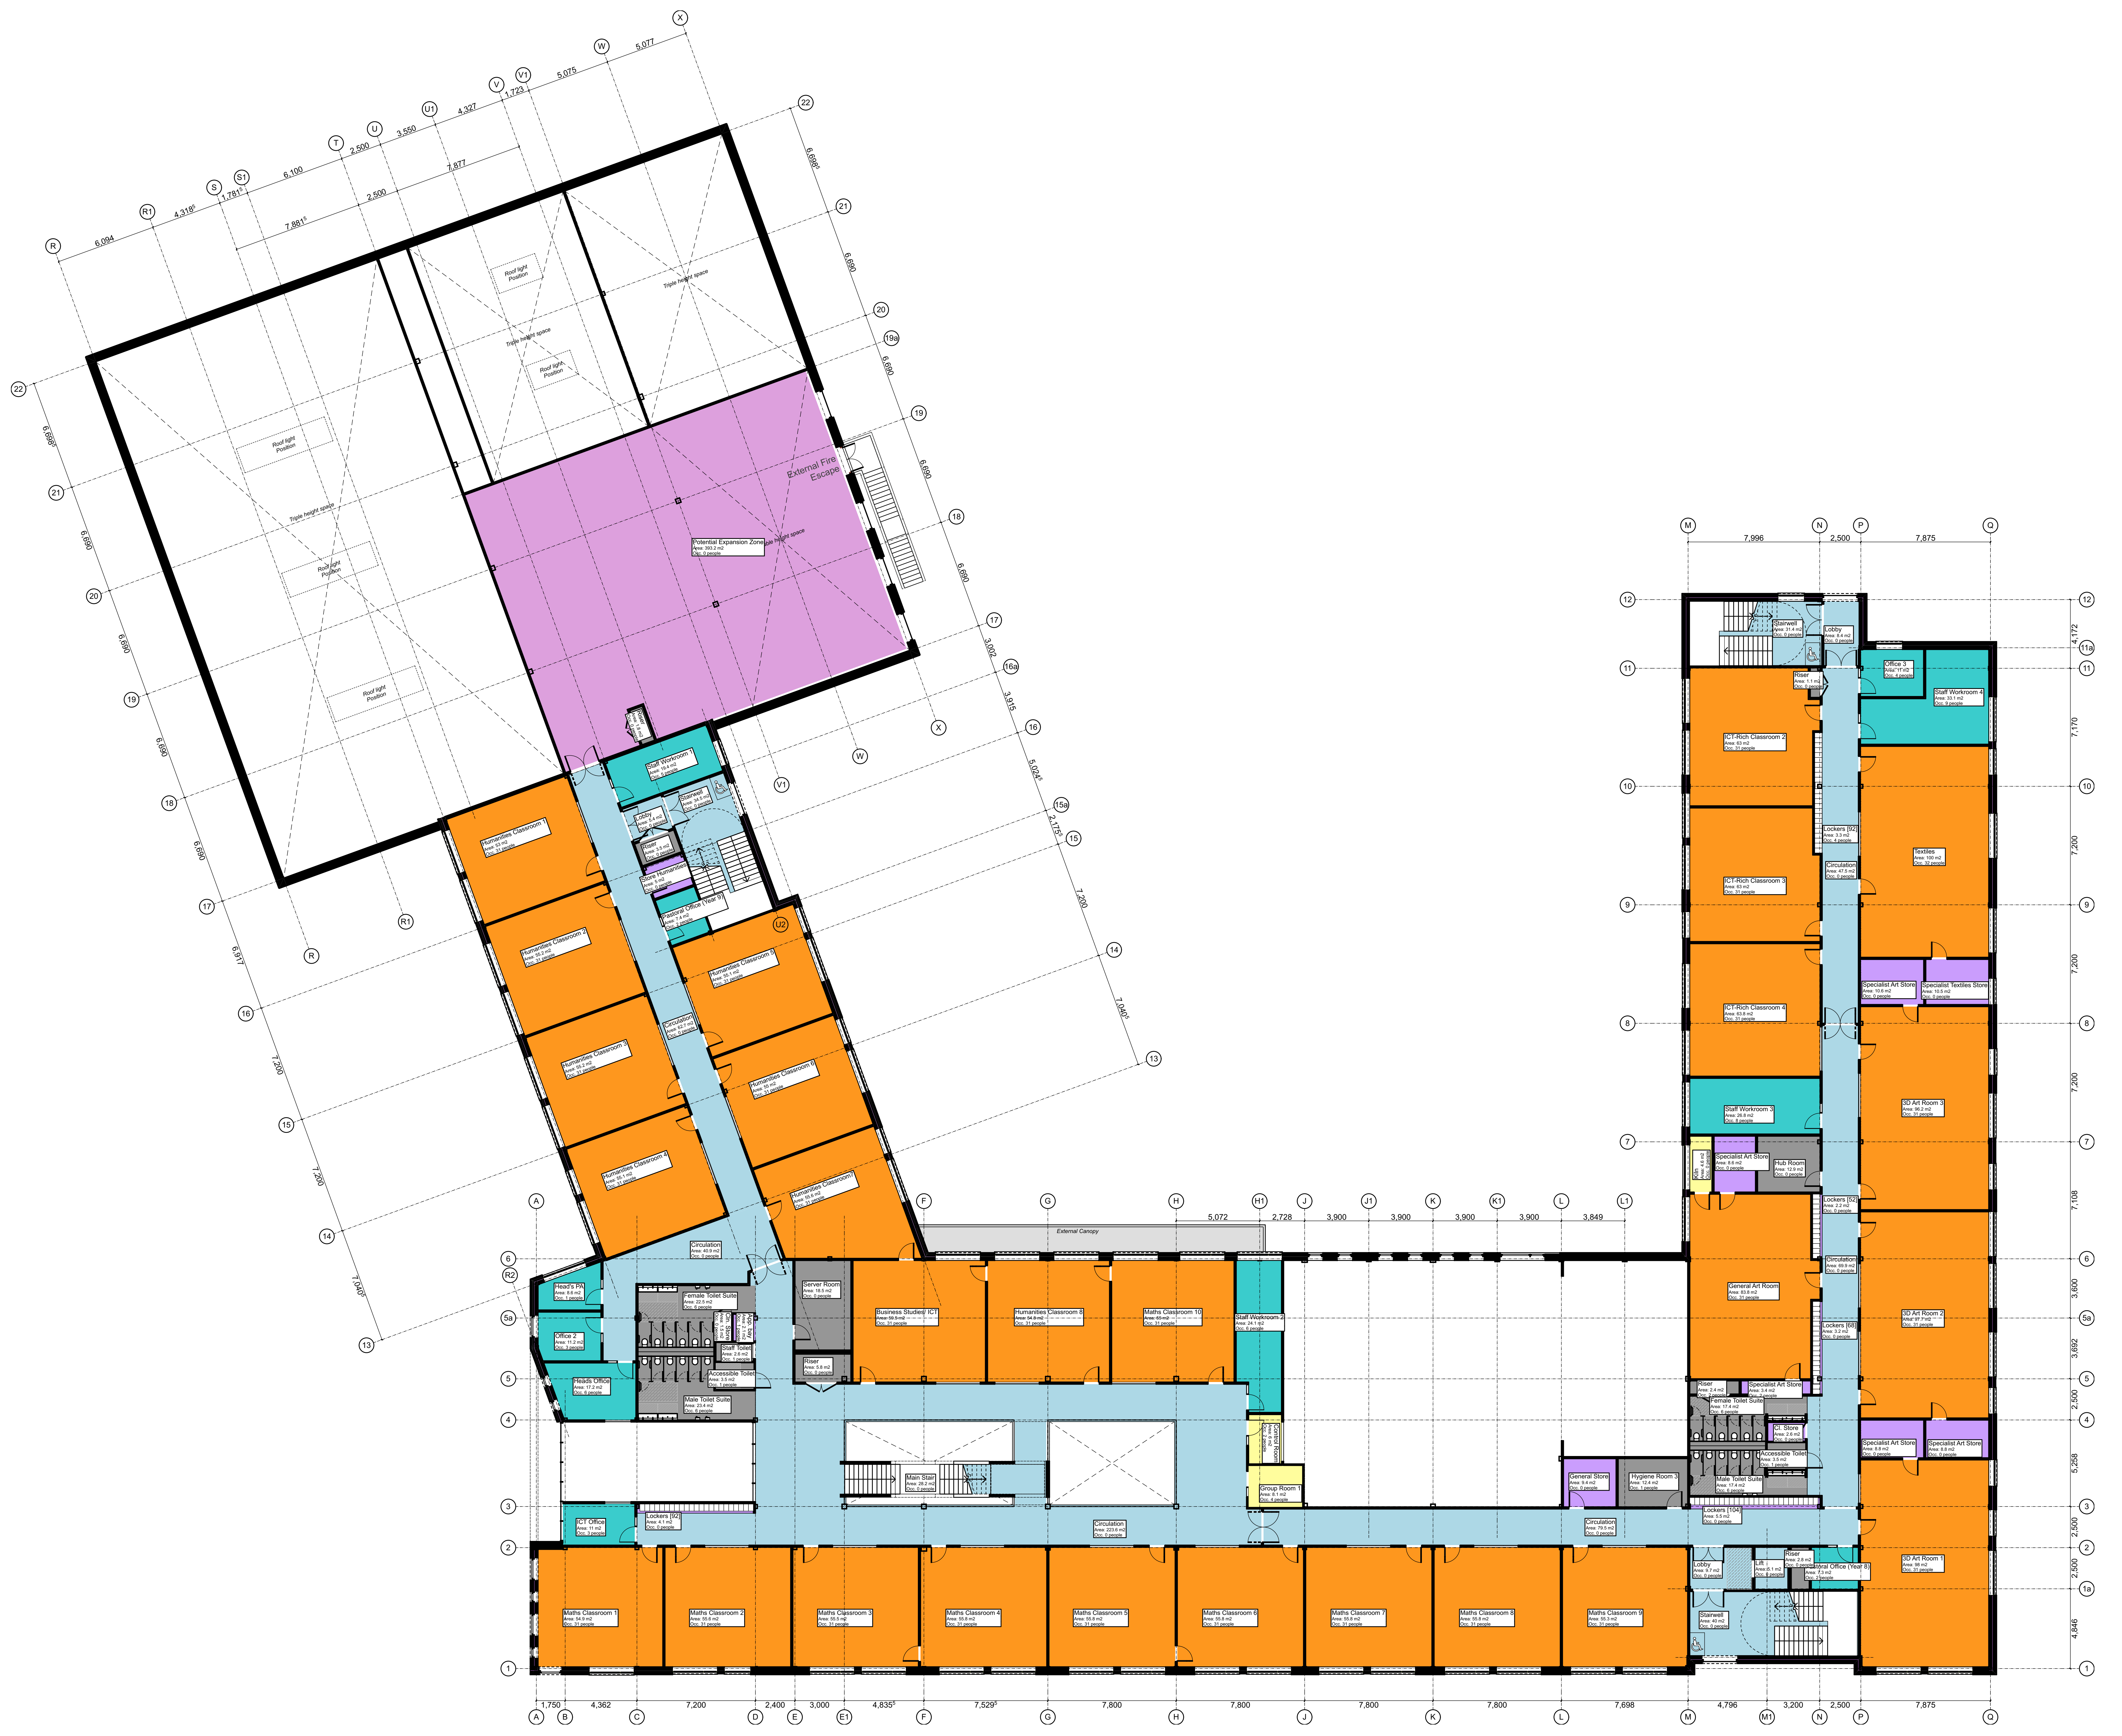
Potential Expansion Zone Area: 393.2 m2 Occ. 0 people
External Fire Escape
Triple height space
Roof light Position
Riser Area: 1.8 m2 Occ. 0 people
Staff Workroom 1 Area: 19.4 m2 Occ. 5 people
Stairwell Area: 34.5 m2 Occ. 0 people
Lobby Area: 5.4 m2 Occ. 0 people
Riser Area: 3.5 m2 Occ. 0 people
Store Humanities Area: 5 m2 Occ. 0 people
Pastoral Office (Year 9) Area: 7.4 m2 Occ. 2 people
Humanities Classroom 1 Area: 53 m2 Occ. 31 people
Humanities Classroom 2 Area: 55.2 m2 Occ. 31 people
Humanities Classroom 3 Area: 55.2 m2 Occ. 31 people
Humanities Classroom 4 Area: 55.1 m2 Occ. 31 people
Humanities Classroom 5 Area: 55.1 m2 Occ. 31 people
Humanities Classroom 6 Area: 55 m2 Occ. 31 people
Humanities Classroom7 Area: 55.6 m2 Occ. 31 people
Circulation Area: 62.7 m2 Occ. 0 people
Circulation Area: 40.9 m2 Occ. 0 people
External Canopy
Head's PA Area: 8.6 m2 Occ. 1 people
Office 2 Area: 11.2 m2 Occ. 3 people
Heads Office Area: 17.2 m2 Occ. 6 people
Female Toilet Suite Area: 22.5 m2 Occ. 6 people
Cln. Store Area: 1.5 m2 Occ. 0 people
App. bay Area: 2.1 m2 Occ. 1 people
Staff Toilet Area: 2.6 m2 Occ. 1 people
Accessible Toilet Area: 3.5 m2 Occ. 1 people
Male Toilet Suite Area: 23.4 m2 Occ. 6 people
Server Room Area: 18.5 m2 Occ. 0 people
Riser Area: 5.8 m2 Occ. 0 people
Business Studies/ ICT Area: 59.5 m2 Occ. 31 people
Humanities Classroom 8 Area: 54.8 m2 Occ. 31 people
Maths Classroom 10 Area: 55 m2 Occ. 31 people
Staff Workroom 2 Area: 24.1 m2 Occ. 6 people
Control Room Area: 6 m2 Occ. 2 people
Group Room 1 Area: 8.1 m2 Occ. 4 people
Main Stair Area: 28.2 m2 Occ. 0 people
ICT Office Area: 11 m2 Occ. 3 people
Lockers [92] Area: 4.1 m2 Occ. 0 people
Circulation Area: 223.6 m2 Occ. 0 people
Maths Classroom 1 Area: 54.9 m2 Occ. 31 people
Maths Classroom 2 Area: 55.6 m2 Occ. 31 people
Maths Classroom 3 Area: 55.5 m2 Occ. 31 people
Maths Classroom 4 Area: 55.8 m2 Occ. 31 people
Maths Classroom 5 Area: 55.8 m2 Occ. 31 people
Maths Classroom 6 Area: 55.8 m2 Occ. 31 people
Maths Classroom 7 Area: 55.8 m2 Occ. 31 people
Maths Classroom 8 Area: 55.8 m2 Occ. 31 people
Maths Classroom 9 Area: 55.3 m2 Occ. 31 people
General Store Area: 9.4 m2 Occ. 0 people
Hygiene Room 3 Area: 12.4 m2 Occ. 1 people
Circulation Area: 79.5 m2 Occ. 0 people
Lockers [104] Area: 5.5 m2 Occ. 0 people
Riser Area: 2.4 m2 Occ. 2 people
Specialist Art Store Area: 3.4 m2 Occ. 2 people
Female Toilet Suite Area: 17.4 m2 Occ. 6 people
Cl. Store Area: 2.6 m2 Occ. 0 people
Accessible Toilet Area: 3.5 m2 Occ. 1 people
Male Toilet Suite Area: 17.4 m2 Occ. 6 people
Lobby Area: 9.7 m2 Occ. 0 people
Lift Area: 5.1 m2 Occ. 0 people
Riser Area: 2.8 m2 Occ. 0 people
Pastoral Office (Year 8) Area: 7.3 m2 Occ. 2 people
Stairwell Area: 40 m2 Occ. 0 people
3D Art Room 1 Area: 98 m2 Occ. 31 people
Specialist Art Store Area: 8.8 m2 Occ. 0 people
Specialist Art Store Area: 8.8 m2 Occ. 0 people
3D Art Room 2 Area: 97.7 m2 Occ. 31 people
General Art Room Area: 83.8 m2 Occ. 31 people
Lockers [68] Area: 3.2 m2 Occ. 0 people
Circulation Area: 69.9 m2 Occ. 0 people
Lockers [52] Area: 2.2 m2 Occ. 0 people
Kiln Area: 4.6 m2 Occ. 0 people
Specialist Art Store Area: 8.6 m2 Occ. 0 people
Hub Room Area: 12.9 m2 Occ. 0 people
Staff Workroom 3 Area: 26.8 m2 Occ. 8 people
3D Art Room 3 Area: 96.2 m2 Occ. 31 people
ICT-Rich Classroom 4 Area: 63.8 m2 Occ. 31 people
Specialist Art Store Area: 10.6 m2 Occ. 0 people
Specialist Textiles Store Area: 10.5 m2 Occ. 0 people
Textiles Area: 100 m2 Occ. 32 people
ICT-Rich Classroom 3 Area: 63 m2 Occ. 31 people
Circulation Area: 47.5 m2 Occ. 0 people
Lockers [92] Area: 3.3 m2 Occ. 4 people
ICT-Rich Classroom 2 Area: 63 m2 Occ. 31 people
Riser Area: 1.1 m2 Occ. 0 people
Office 3 Area: 11 m2 Occ. 4 people
Staff Workroom 4 Area: 33.1 m2 Occ. 9 people
Stairwell Area: 31.4 m2 Occ. 0 people
Lobby Area: 8.4 m2 Occ. 0 people
A B C D E E1 F G H H1 J J1 K K1 L L1 M M1 N P Q R R1 S S1 T U U1 V V1 W X U2 R2
1 1a 2 3 4 5 5a 6 7 8 9 10 11 11a 12 13 14 15 15a 16 16a 17 18 19 19a 20 21 22
1,750 4,362 7,200 2,400 3,000 4,835 7,529 7,800 7,800 7,800 7,800 7,698 4,796 3,200 2,500 7,875
5,072 2,728 3,900 3,900 3,900 3,900 3,849
7,996 2,500 7,875
4,172 7,170 7,200 7,200 7,200 7,108 3,600 3,692 2,500 5,258 2,500 2,500 4,846
6,094 4,318 1,781 6,100 2,500 3,550 4,327 1,723 5,075 5,077 7,881 2,500 1,877
6,690 6,690 6,690 6,690 6,690 3,002 3,815 5,054 2,175 7,200 7,040 6,917 7,200 7,200 7,509

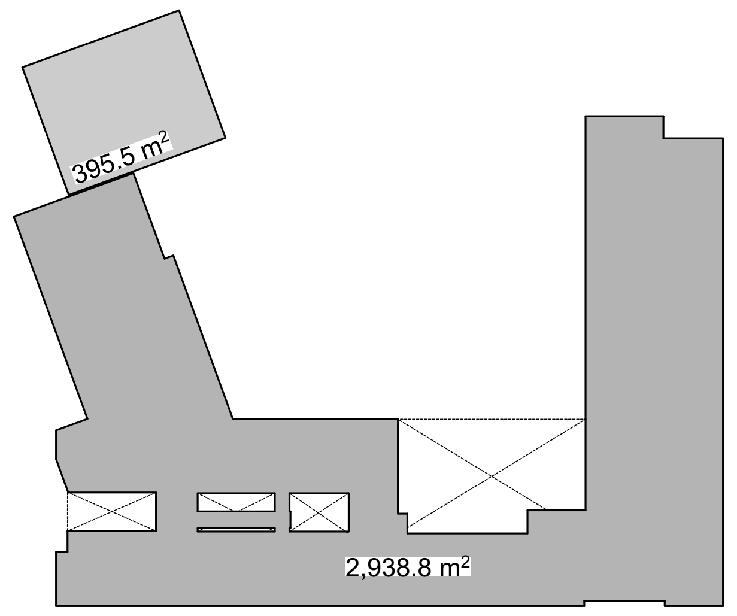

GIFA

Ground Floor: 4746.7 m²

1st Floor: 2938.8 m²

2nd Floor: 3361.9 m²

Total GIFA: 11047.4 m²

Proposed Expansion Zone: 393.2 m²

Plant Area: 75.3 m²

rev	description	drawn	checked	date
P01	First issue	RR	AM	13.02.2020

BOND BRYAN
The Church Studio Springvale Road Sheffield S10 1LP
t +44(0)114 266 2040 w www.bondbryan.com
e BPTC@bondbryan.co.uk

Benton Park School
Harrogate Road, Rawdon, Leeds, LS19 6LX

BAM Construction

FIRST FLOOR GA PLAN

bba project ref	scale(s)	original paper size
16-157A	1:200	A1

name :

project	originator	volume	level	type	role	number
BPS	BBA	ZZ	01	DR	A	2001

status : S2
suitability description : **SUITABLE FOR INFORMATION**
revision : P01
revision description : **PRELIMINARY**

This document is © Bond Bryan Architects Ltd. If in doubt ASK. Drawing measurements shall not be obtained by scaling. Verify all dimensions prior to construction. Immediately report any discrepancies on this document to the Architect. This document shall be read in conjunction with associated models, specifications and related consultant's documents.