


Section 01 - Hub - LIC, Main Hall, & Dining

1:100

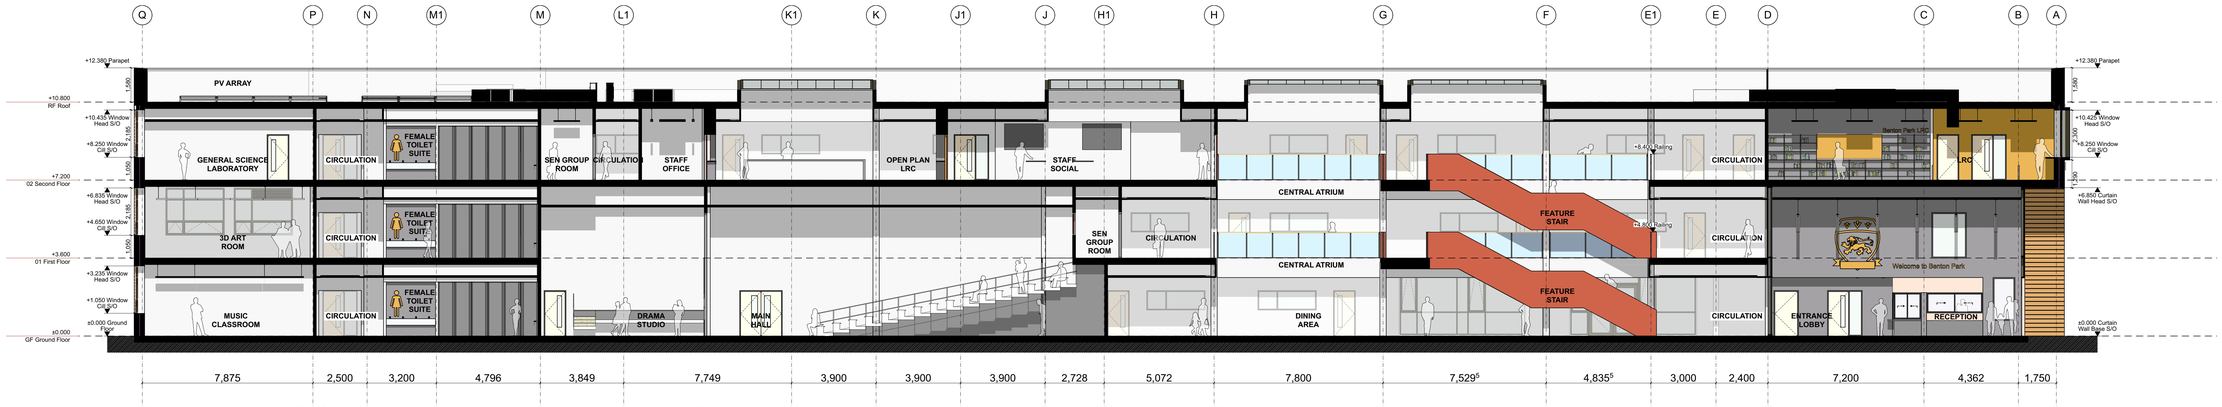

Section 02 - Hub - Drama, Atrium, & LIC


1:100



Section 03 - East Wing - Arts, Science, & Circulation

1:100

KEY PLAN

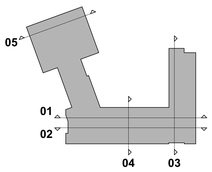

rev	description	drawn	checked	date
P01	First issue	RR	AM	14.02.2020

BOND BRYAN

The Church Studio Springvale Road Sheffield S10 1LP

t +44(0)114 266 2040 w www.bondbryan.com

e BPTC@bondbryan.co.uk

Benton Park School

Harrogate Road, Rawdon, Leeds, LS19 6LX

BAM Construction

GA SECTIONS SHEET 1

bba project ref	scale(s)	original paper size
16-157A	1:100	A0

name :

project	originator	volume	level	type	role	number
BPS	BBA	00	ZZ	DR	A	4001

status : suitability description :

S2 **SUITABLE FOR INFORMATION**

revision : revision description :

P01 **PRELIMINARY**

This document is © Bond Bryan Architects Ltd. If in doubt ASK. Drawing measurements shall not be obtained by scaling. Verify all dimensions prior to construction. Immediately report any discrepancies on this document to the Architect. This document shall be read in conjunction with associated models, specifications and related consultant's documents.